0 10 20 30 40 50 100 150 200 250 Mtr.

SCALE -1CM = 10M., RF 1 : 1000

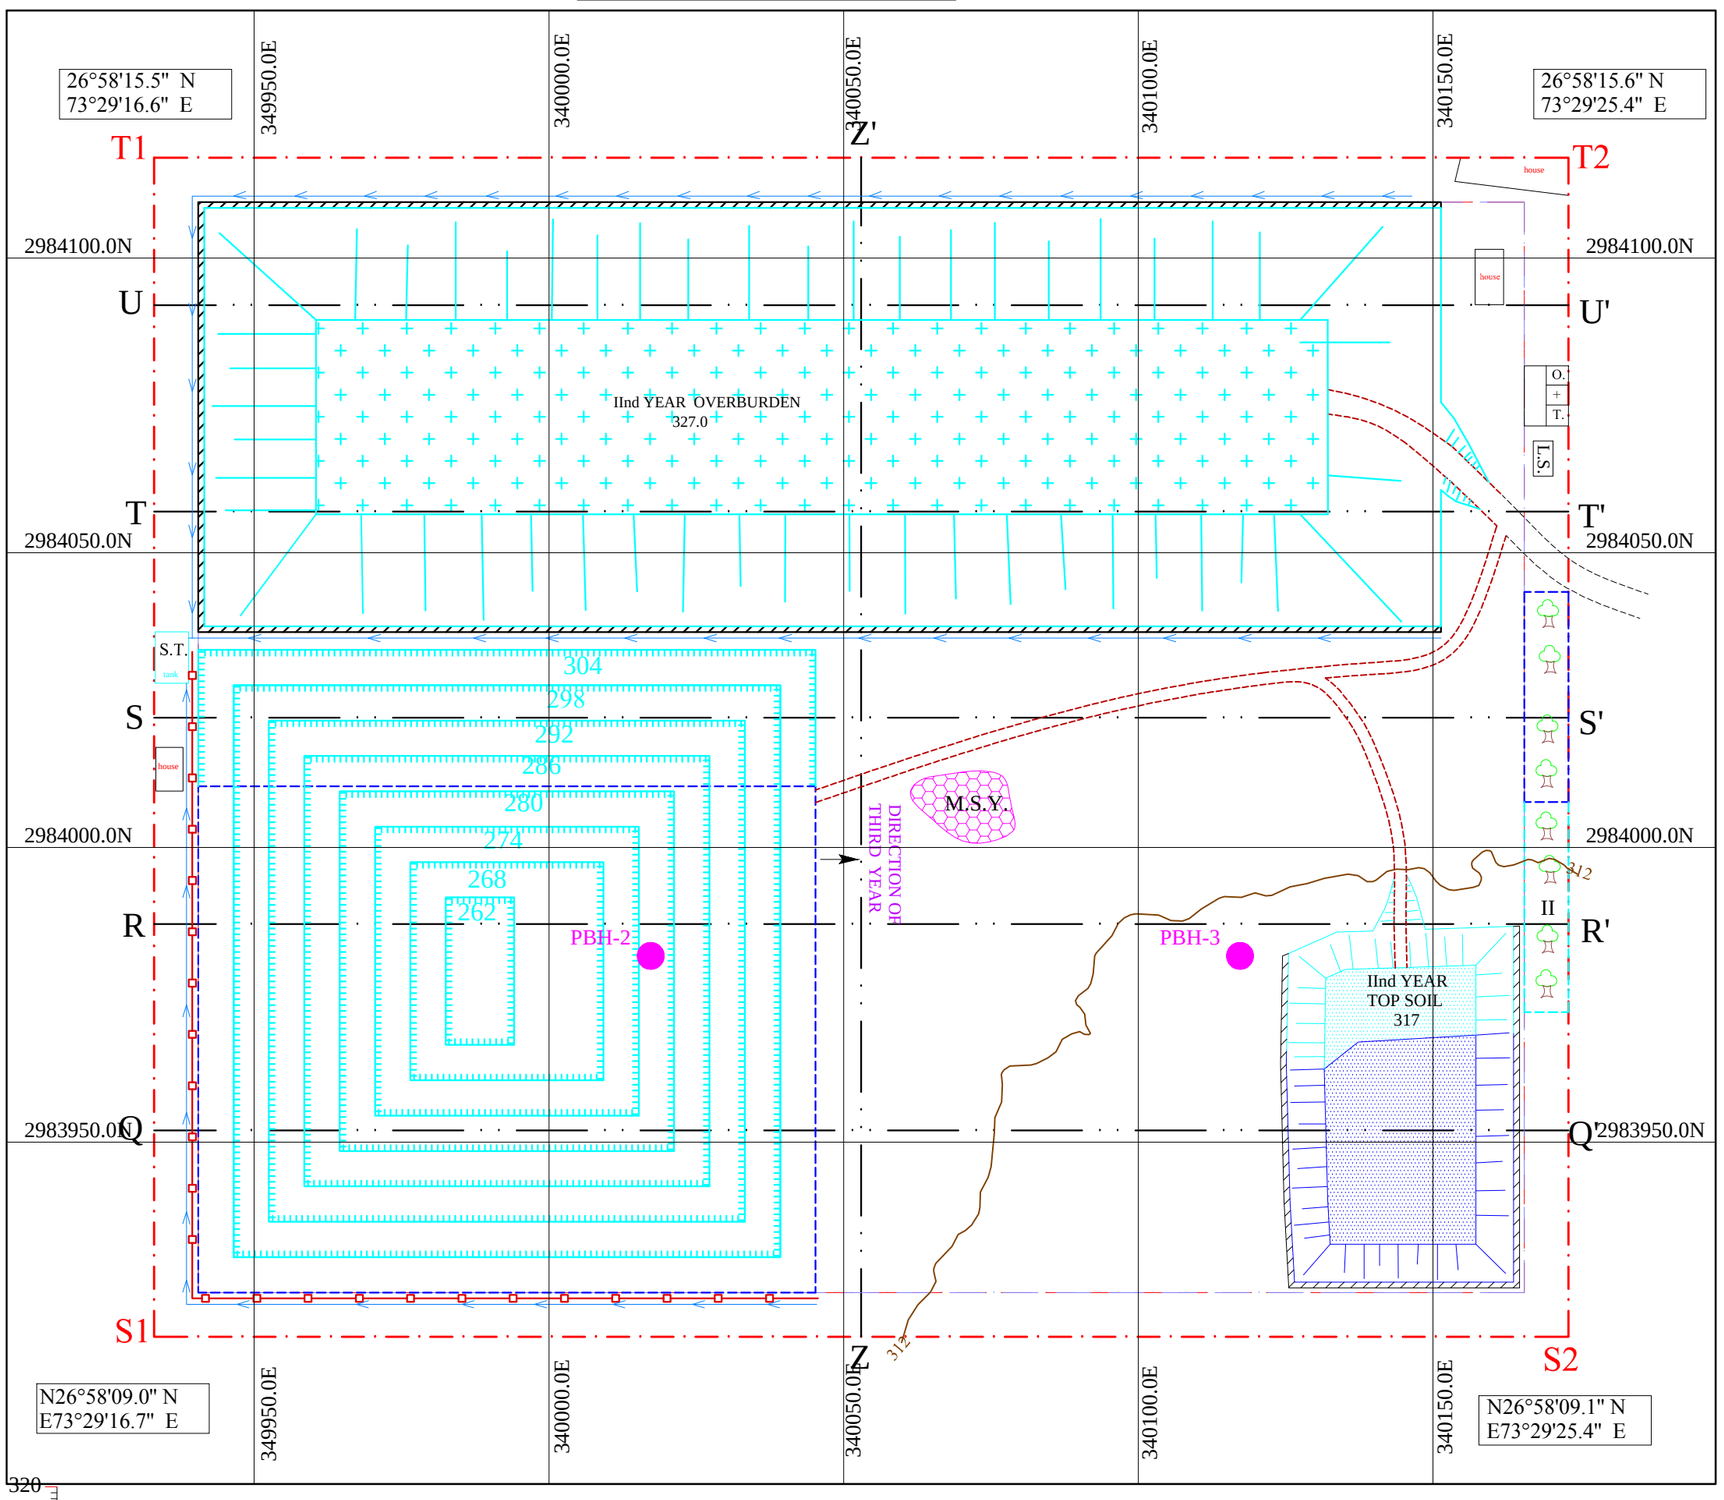

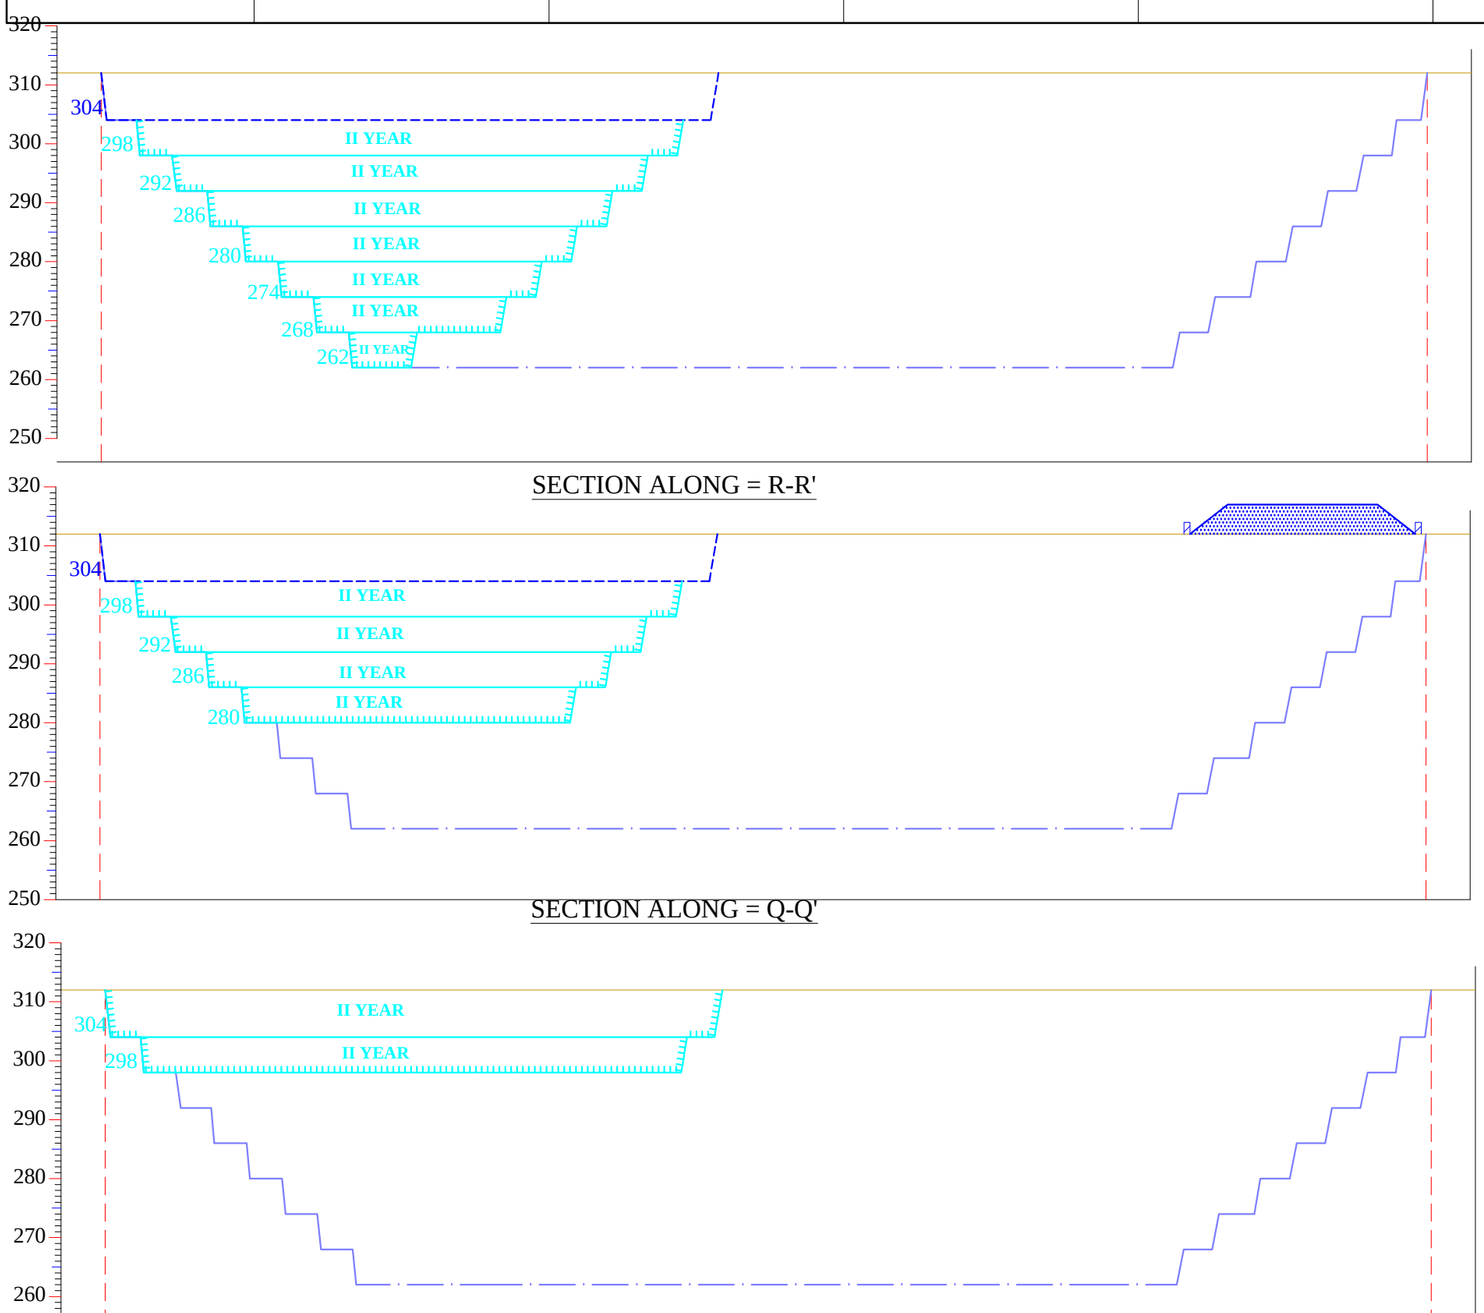

SECTION ALONG = R-R'

SECTION ALONG = Q-Q'

SECTION ALONG = S-S'

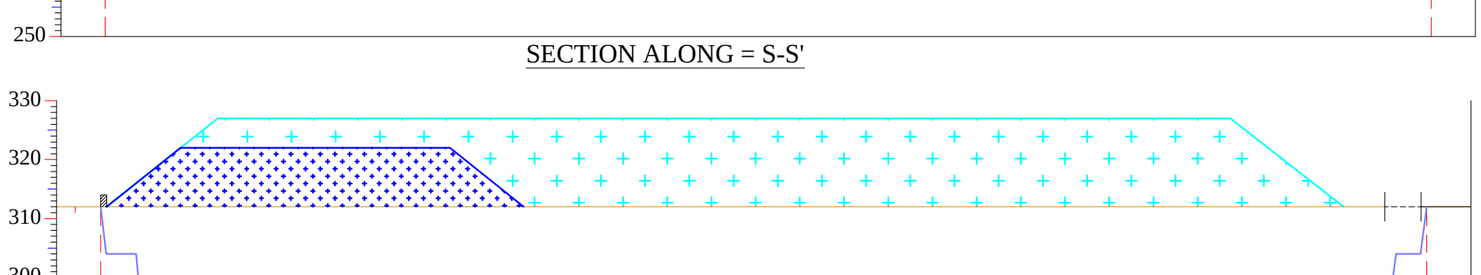

SECTION ALONG = T-T'

SECTION ALONG = U-U'

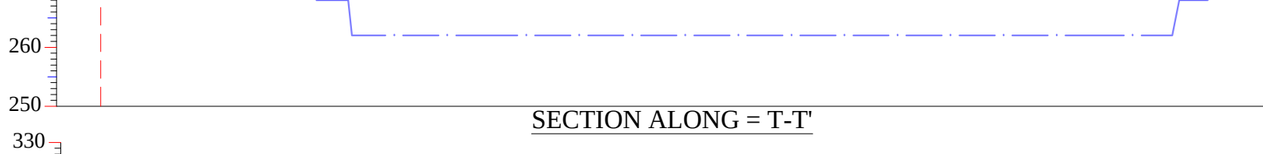

SECTION ALONG = Z-Z'

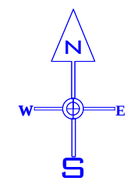

DRONE SURVEY DATE
10 . 03 . 2025

INDEX

	BLOCK BOUNDARY
	7.5M. STATUTORY BARRIER
312	CONTOUR
N26°58'09.1" N E73°29'25.4" E	GEO-COORDINATES (S2 Pillar)
0E 0N 0N	GRID LINE (UTM WGS 84)
	ROAD / RASTA
R R'	SECTION LINE
	EXISTING INFRASTRUCTURE
	ULTIMATE PIT LIMIT
	PROP. MINERAL STACK YARD
	PROPOSED RETAINING WALL
	PROP. HAULAGE ROAD (1:16)
	PROPOSED IInd YEAR TOP SOIL STACK YARD
II YEAR	PROP. IInd YEAR MINE WORKING
	PROPOSED IInd YEAR OVERBURDEN
	PROP. IInd YEAR PLANTATION
	PROP. GARLAND DRAIN
S.T.	PROPOSED SETTING TANK
	PROPOSED FENCING
O + T	PROPOSED OFFICE COMPLEX
L. S.	PROPOSED LABOUR SHED
PBH-2	PROPOSED BORE HOLE

PROPOSED IInd YEAR DEVELOPMENT PLAN OF HARIPURA LIMESTONE BLOCK TKSB-18FOR AREA OF 4.800 HECT.

N\v - Haripura, Tehsil -Kheenvsar , Distt.- **Nagaur** (Raj.)
Mineral - Limestone
Applicant - M/s. Suncity Chemical & Minerals Private Limited
Area - 4.800 Hect. , Scale - 1 : 1000

PLATE NO.- 5B

THIS IS CERTIFIED THAT THE PLAN IS PREPARED BASED ON THE BLOCK MAP AUTHENTICATED BY THE STATE GOVT. AND ARE CORRECT TO THE BEST OF MY KNOWLEDGE

Nimish Singhwi
Digitally signed by Nimish Singhwi
Date: 2025.05.31 17:50:27 -07'00'

QUALIFIED PERSON
MINING ENGINEER