


0 10 20 30 40 50 100 150 200 250 Mtr.


SCALE -1CM = 10M., RF 1 : 1000


DRONE SURVEY DATE
10 . 03 . 2025

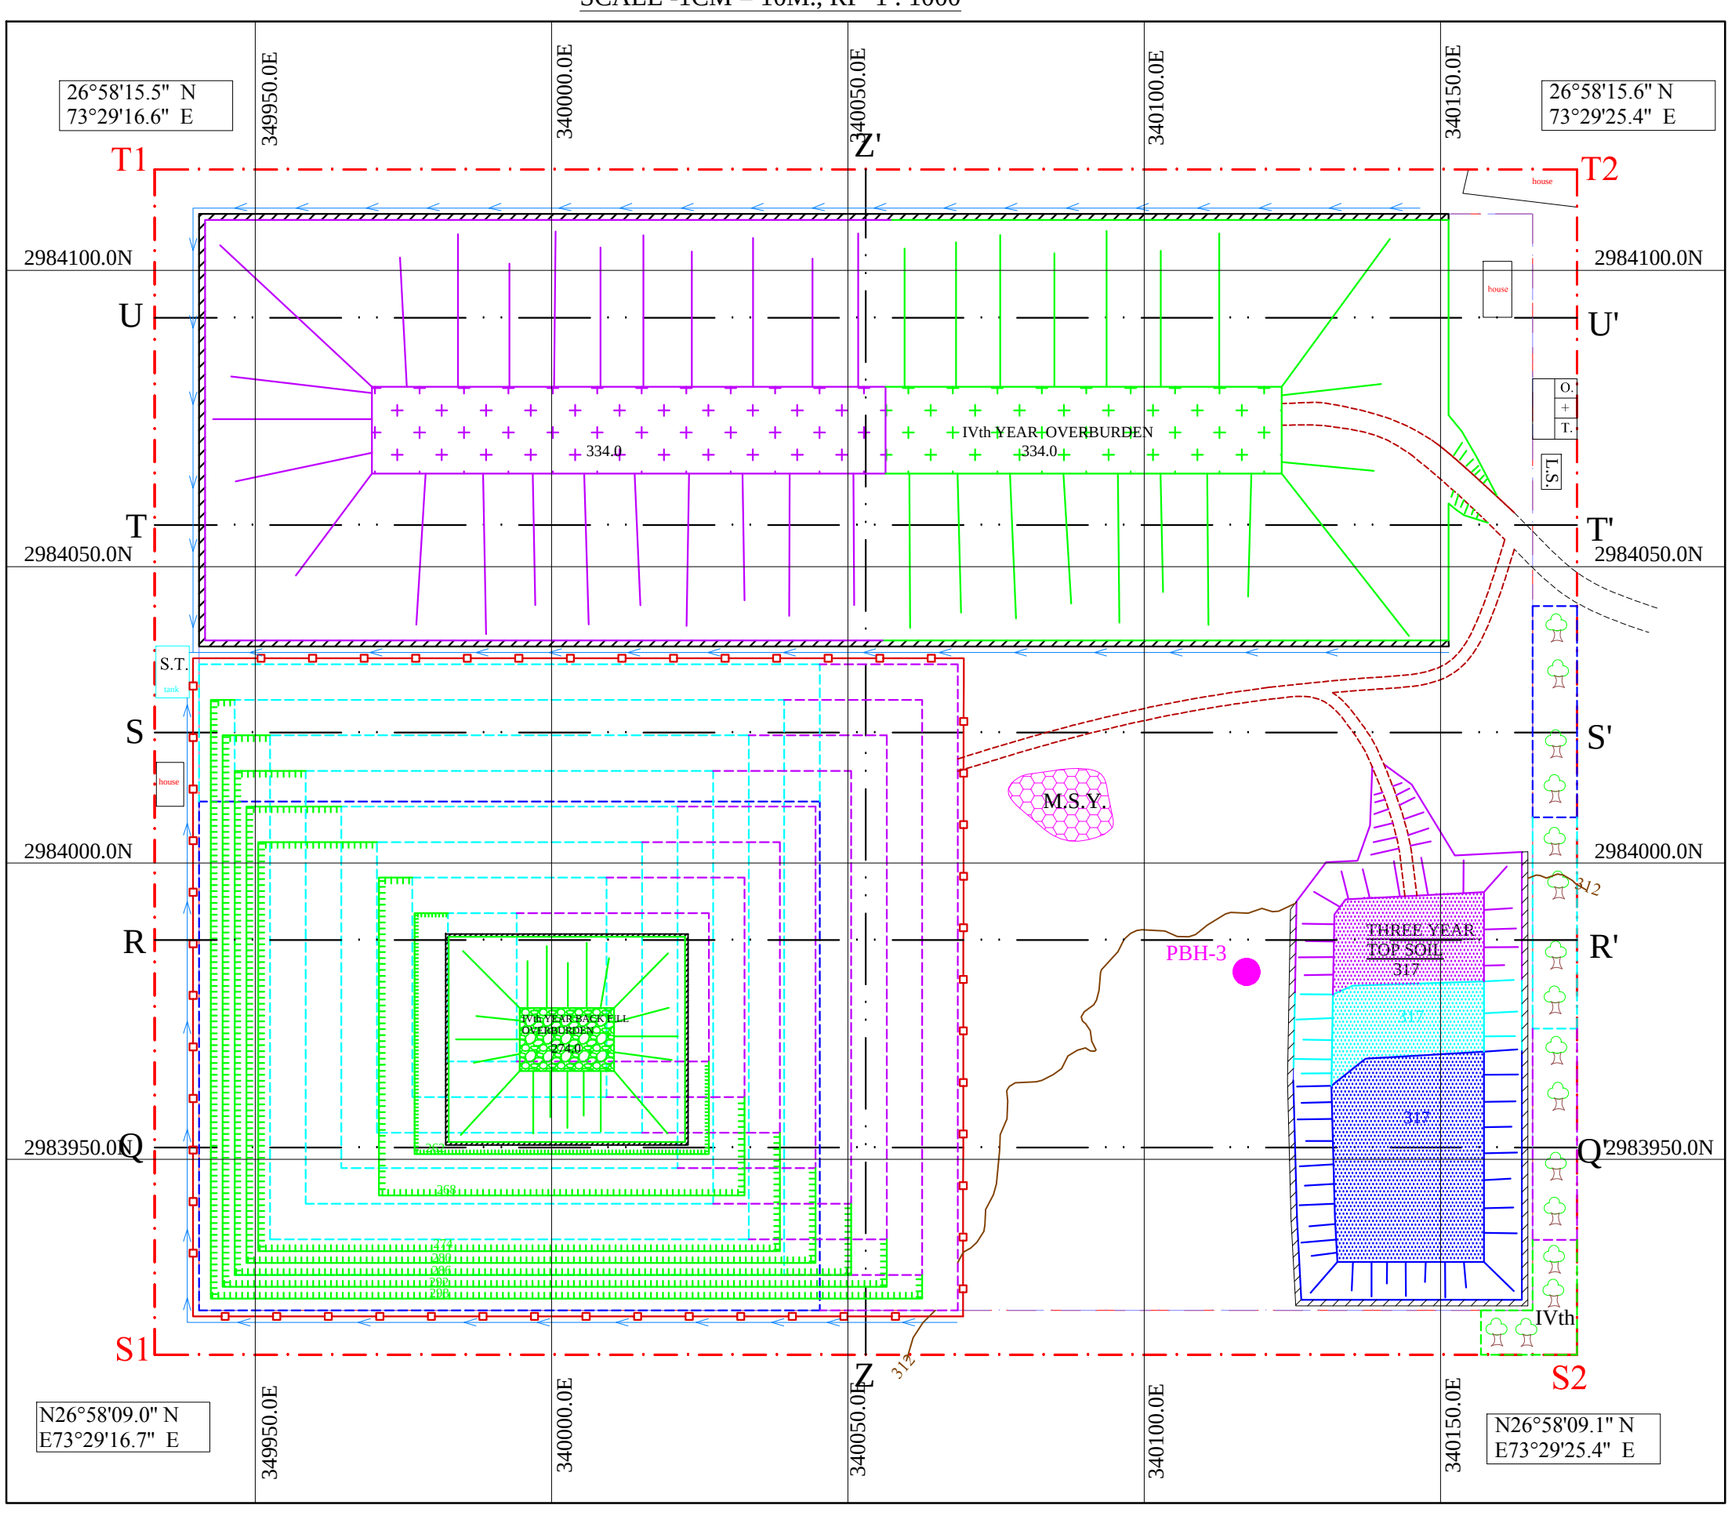


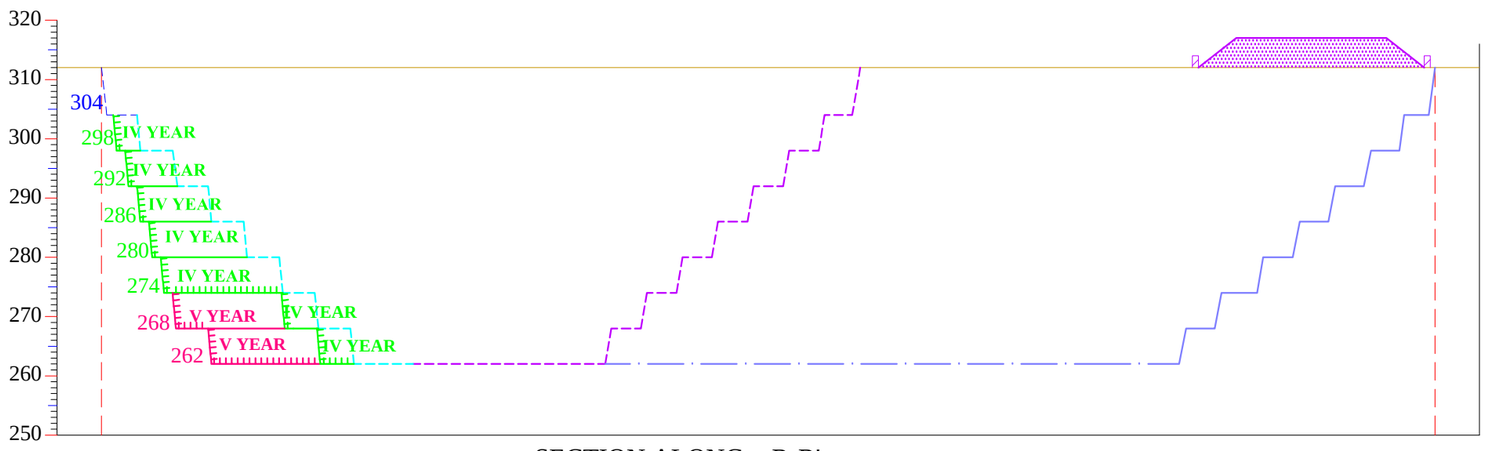


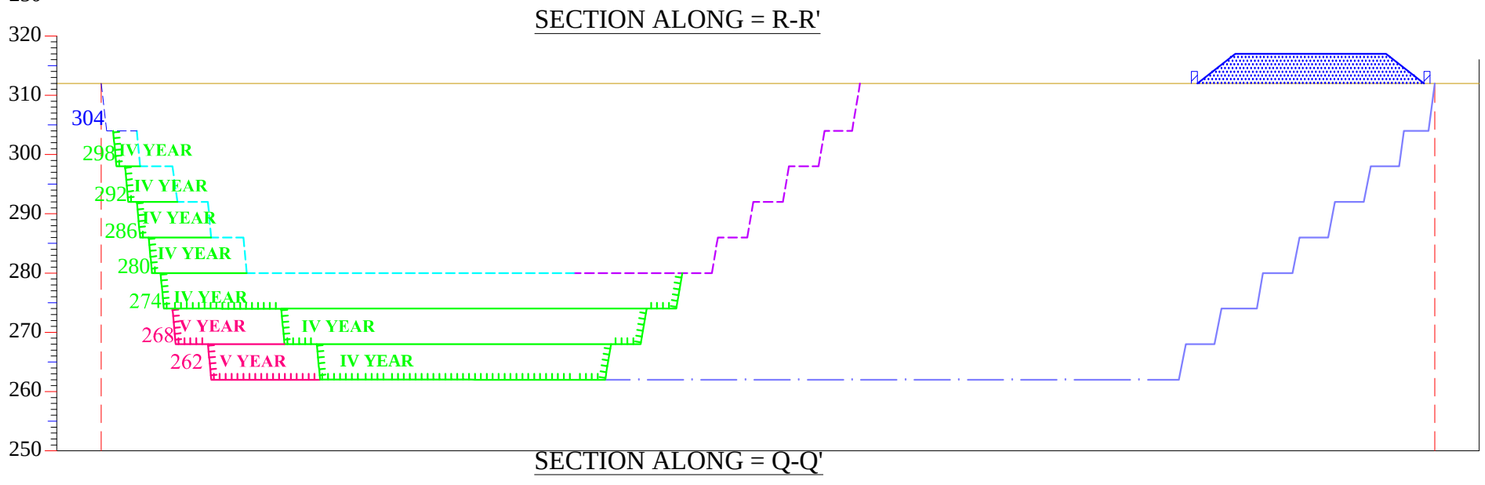

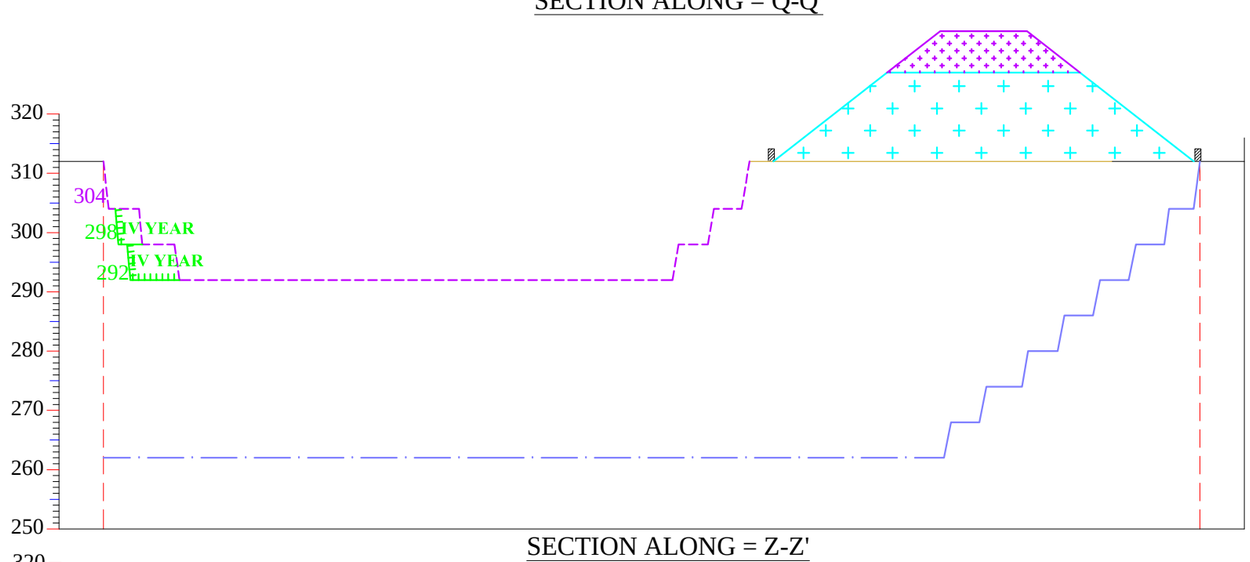

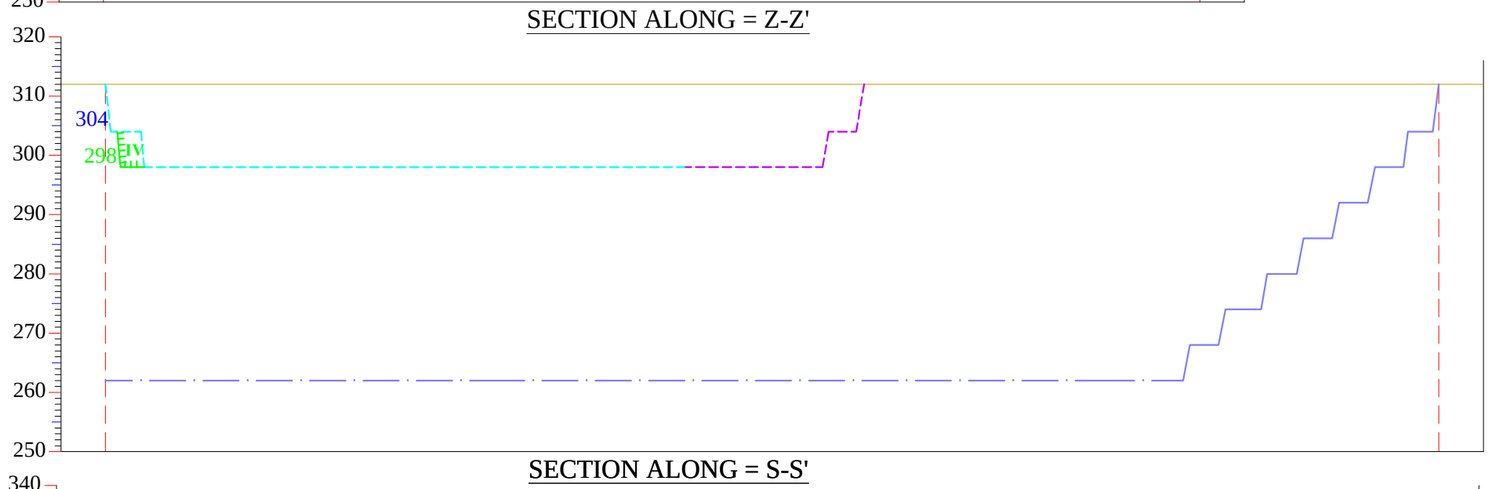

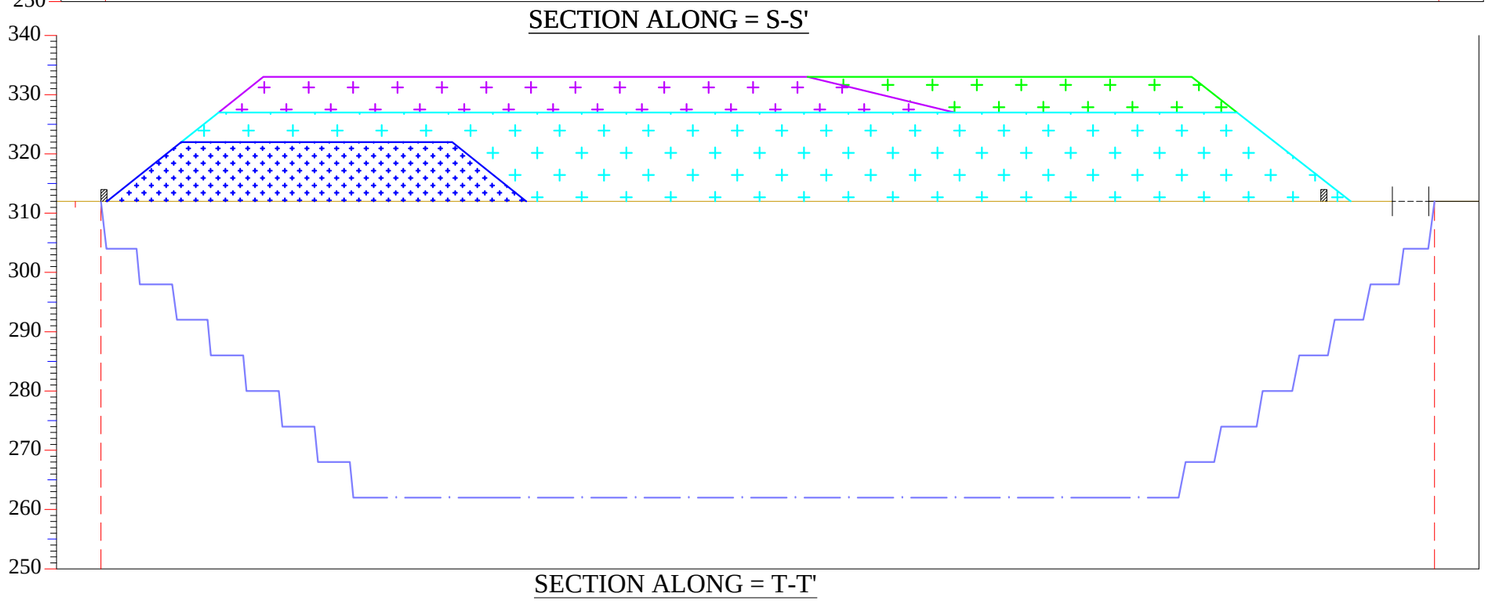

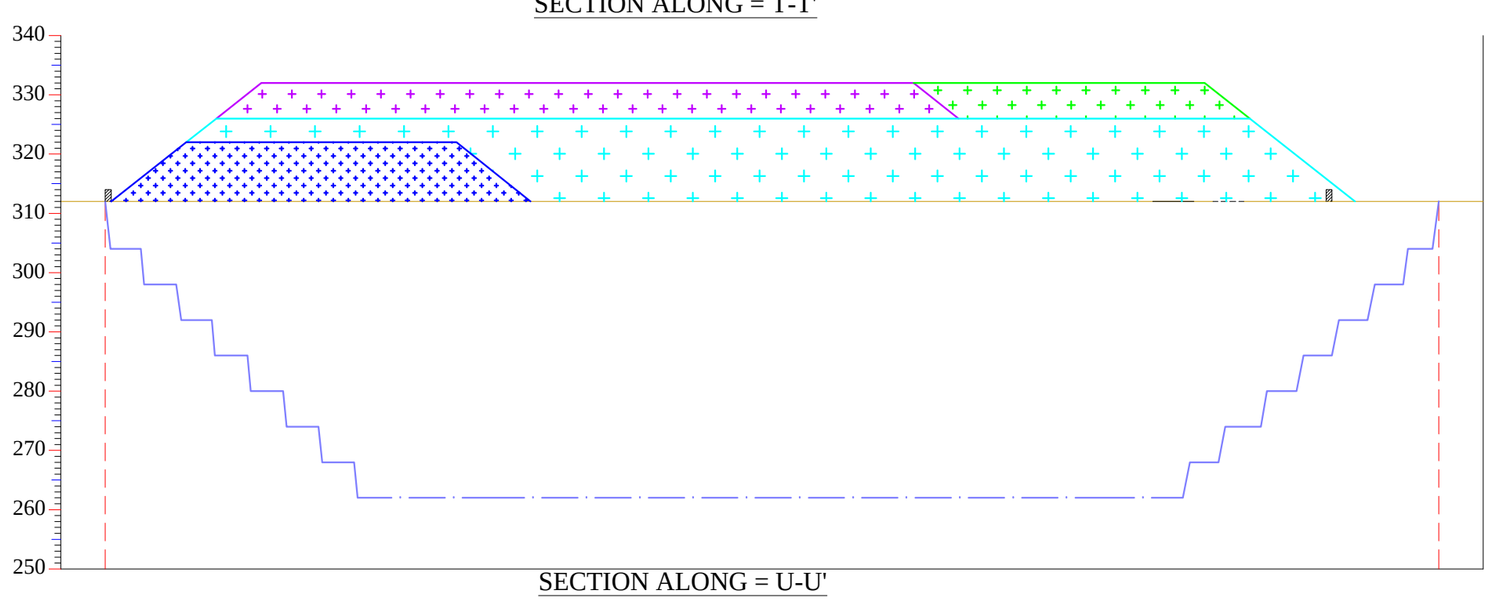

INDEX

	BLOCK BOUNDARY
	7.5M. STATUTORY BARRIER
312	CONTOUR
N26°58'09.1" N E73°29'25.4" E	GEO-COORDINATES (S2 Pillar)
0E 0N 0N	GRID LINE (UTM WGS 84)
0N	ROAD / RASTA
Q Q'	SECTION LINE
	EXISTING INFRASTRUCTURE
	ULTIMATE PIT LIMIT
	PROP. MINERAL STACK YARD
	PROPOSED RETAINING WALL
	PROP. HAULAGE ROAD (1:16)
	PROP. THREE YEAR TOP SOIL STACK YARD
IV YEAR	PROP. IVth YEAR MINE WORKING
	PROPOSED IVth YEAR OVERBURDEN
	PROPOSED IVth BACK FILL OVERBURDEN
	PROP. IVth YEAR PLANTATION
	PROP. GARLAND DRAIN
S.T.	PROPOSED SETTING TANK
	PROPOSED FENCING
O + T	PROPOSED OFFICE COMPLEX
L. S.	PROPOSED LABOUR SHED
PBH-3	PROPOSED BORE HOLE

PROPOSED IVth YEAR DEVELOPMENT PLAN OF HARIPURA LIMESTONE BLOCK TKSB-18FOR AREA OF 4.800 HECT.

N\v - Haripura, Tehsil -Kheenvsar , Distt.- **Nagaur** (Raj.)
Mineral - Limestone
Applicant - M/s. Suncity Chemical & Minerals Private Limited
Area - 4.800 Hect. , Scale - 1 : 1000

PLATE NO.- 5D

THIS IS CERTIFIED THAT THE PLAN IS PREPARED BASED ON THE BLOCK MAP AUTHENTICATED BY THE STATE GOVT. AND ARE CORRECT TO THE BEST OF MY KNOWLEDGE

Nimish Singhwi
Digitally signed by Nimish Singhwi
Date: 2025.05.31 17:51:37 -07'00'

QUALIFIED PERSON
MINING ENGINEER