

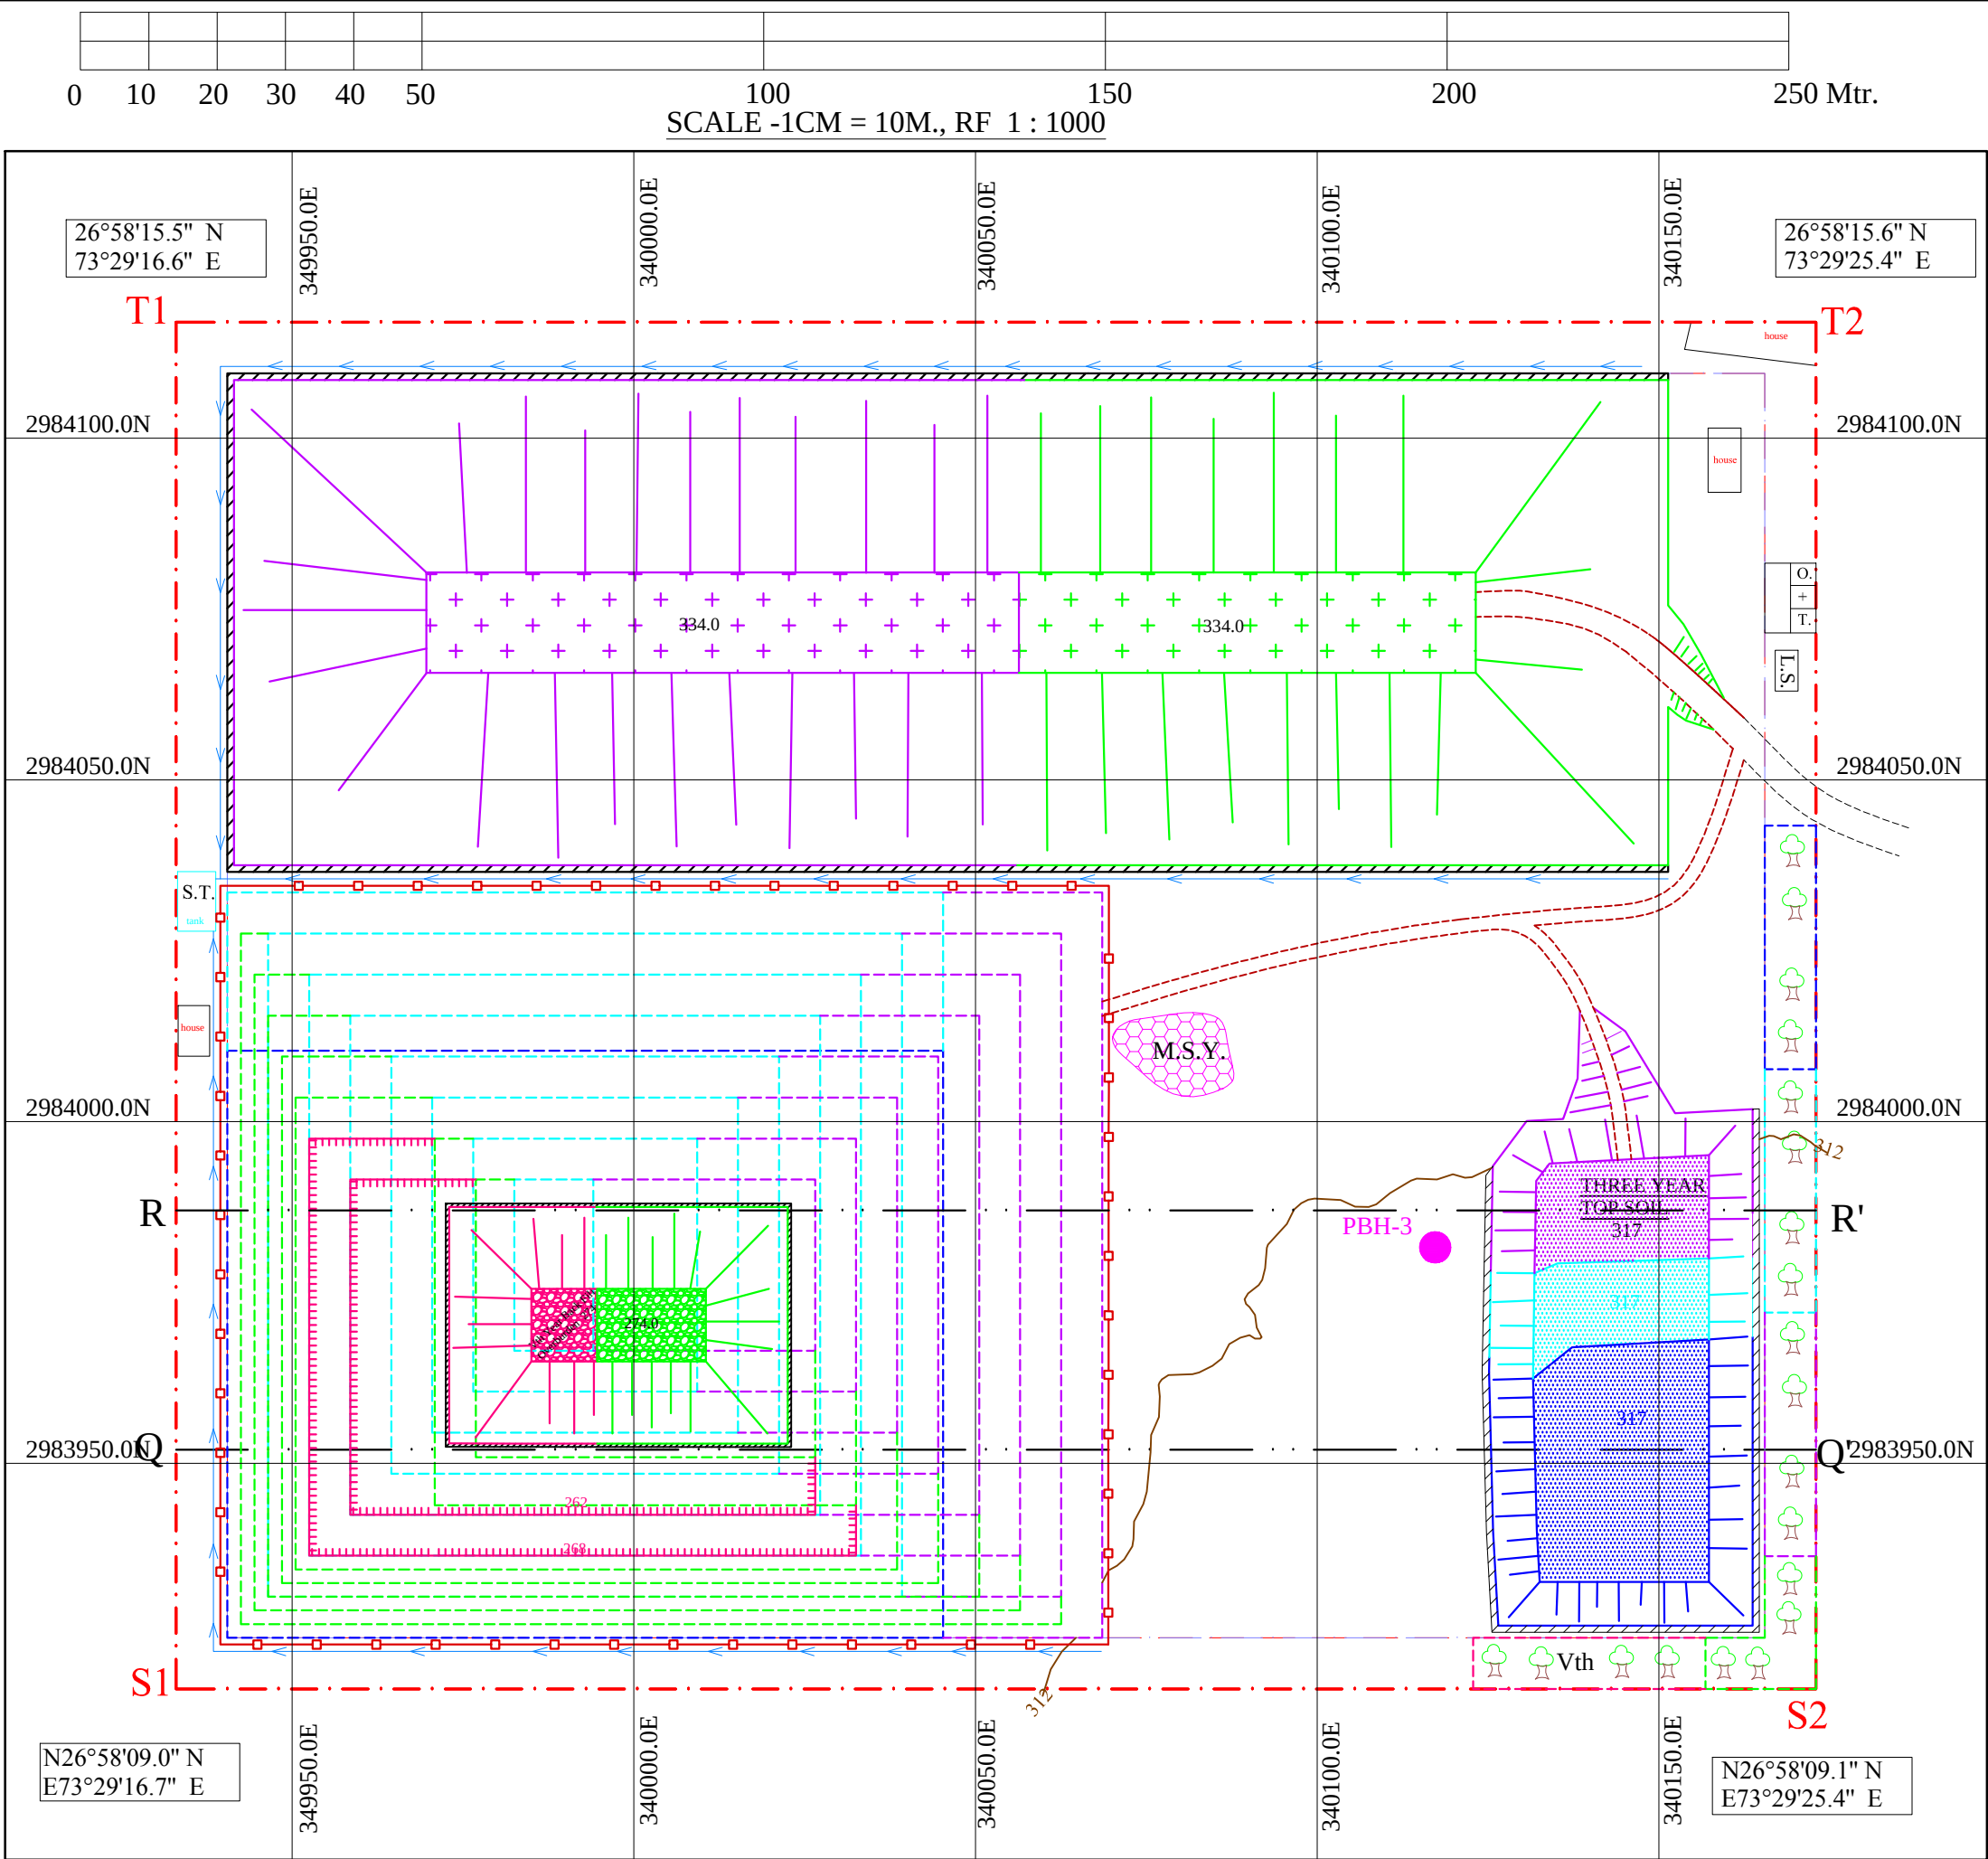


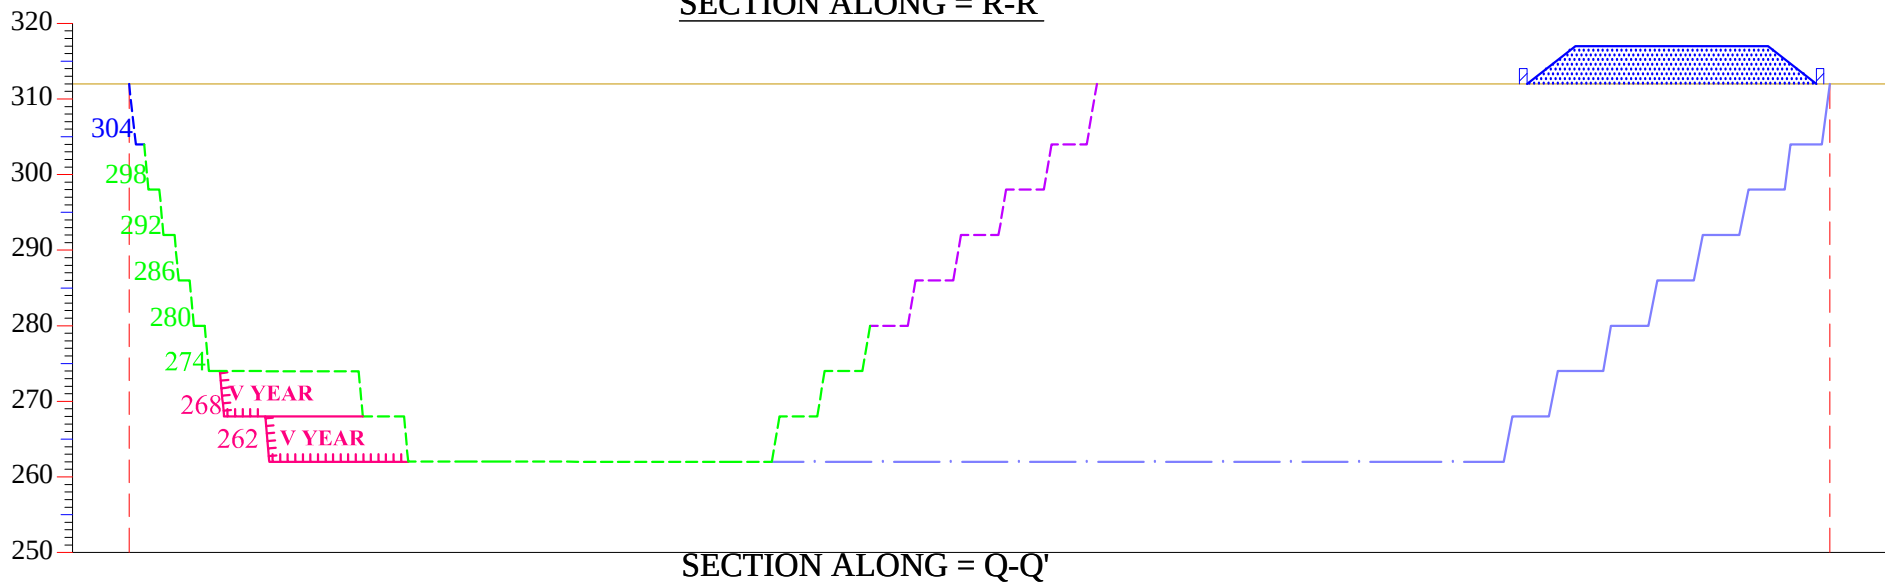

DRONE SURVEY DATE
10 . 03 . 2025

INDEX

	BLOCK BOUNDARY
	7.5M. STATUTORY BARRIER
	CONTOUR
	GEO-COORDINATES (S2 Pillar)
	GRID LINE (UTM WGS 84)
	ROAD / RASTA
	SECTION LINE
	EXISTING INFRASTRUCTURE
	ULTIMATE PIT LIMIT
	PROP. MINERAL STACK YARD
	PROPOSED RETAINING WALL
	PROP. HAULAGE ROAD (1:16)
	PROP. THREE YEAR TOP SOIL STACK YARD
	PROP. Vth YEAR MINE WORKING
	PROPOSED Vth BACK FILL OVERBURDEN
	PROP. Vth YEAR PLANTATION
	PROP. GARLAND DRAIN
	PROPOSED SETTING TANK
	PROPOSED FENCING
	PROPOSED OFFICE COMPLEX
	PROPOSED LABOUR SHED
	PROPOSED BORE HOLE

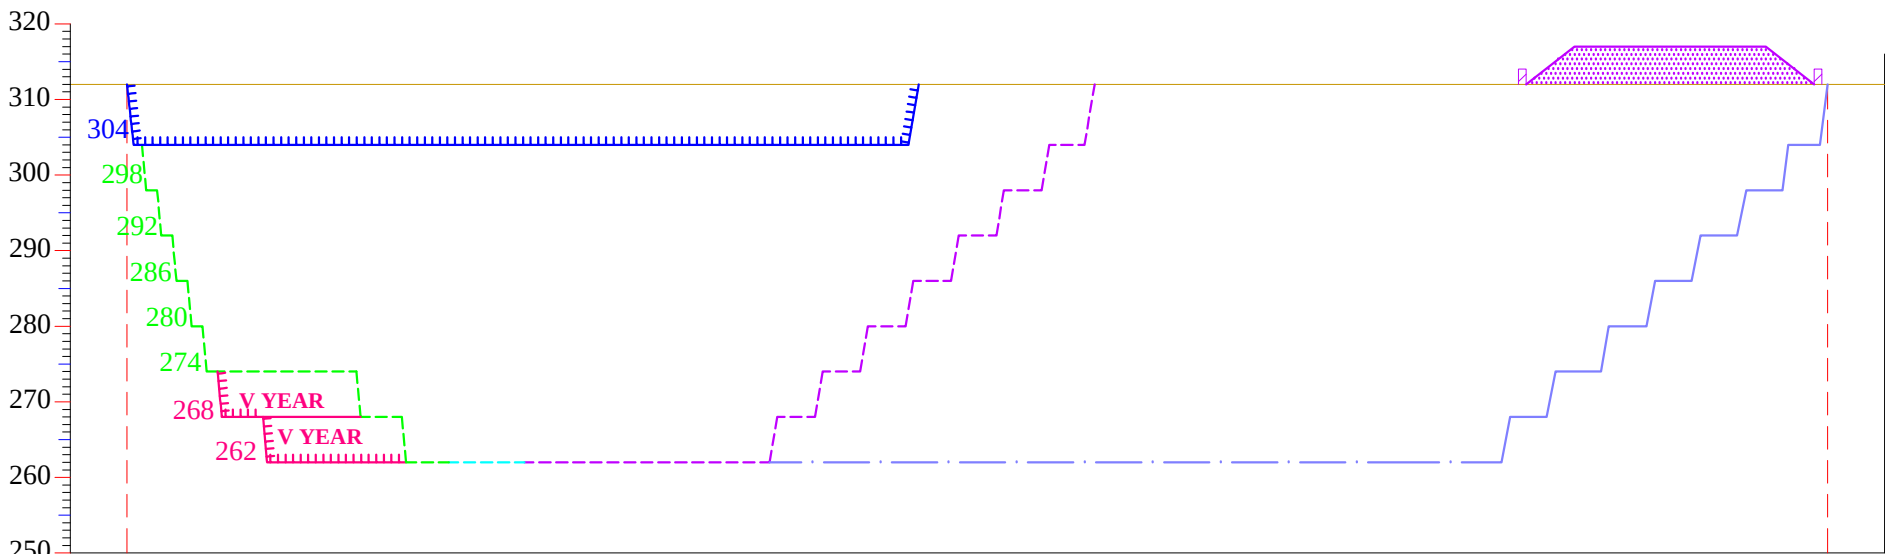

PROPOSED Vth YEAR DEVELOPMENT
PLAN OF HARIPURA LIMESTONE
BLOCK TKSB-18FOR AREA
OF 4.800 HECT.

N\ v - Haripura, Tehsil -Kheenvsar , Distt.- **Nagaur** (Raj.)
Mineral - Limestone
Applicant - M/s. Suncity Chemical &
Minerals Private Limited
Area - 4.800 Hect. , Scale - 1 : 1000

PLATE NO.- 5E

THIS IS CERTIFIED THAT THE PLAN IS PREPARED BASED ON THE BLOCK MAP
AUTHENTICATED BY THE STATE GOVT. AND ARE CORRECT TO THE BEST OF MY KNOWLEDGE

Nimish
Singhwi

Digitally signed
by Nimish
Singhwi
Date: 2025.05.31
17:52:09 -07'00'

QUALIFIED PERSON
MINING ENGINEER