
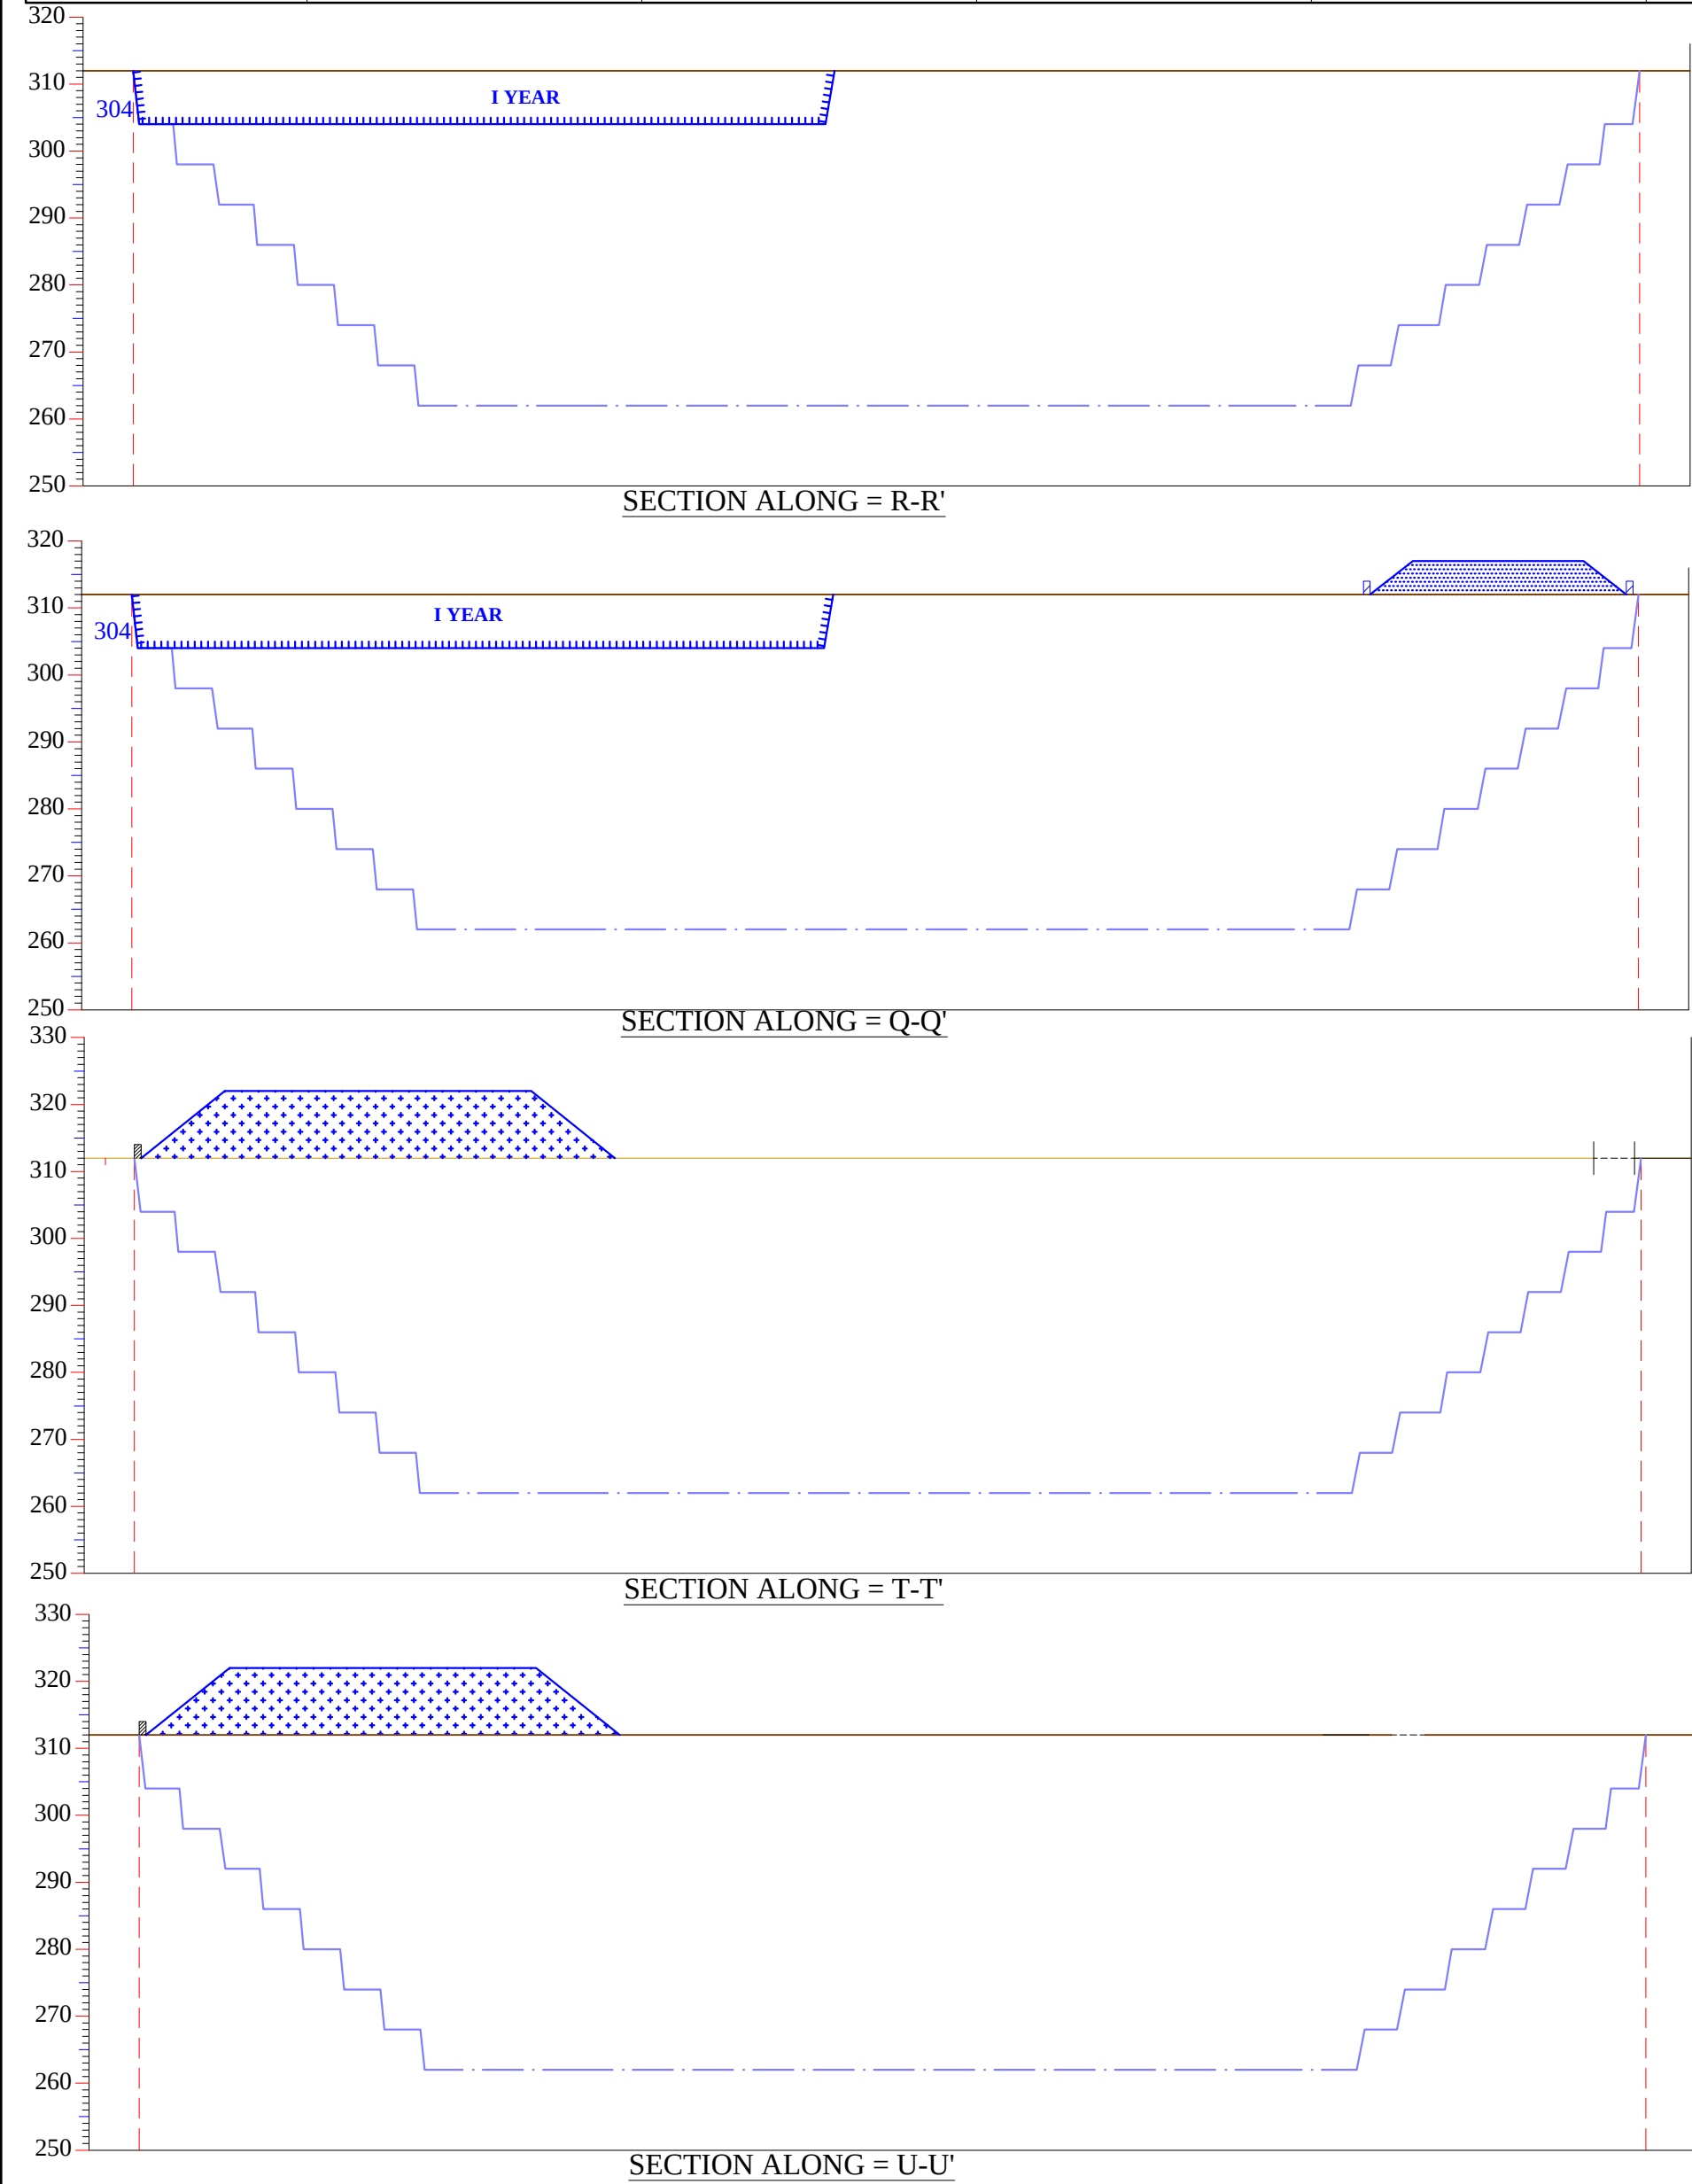


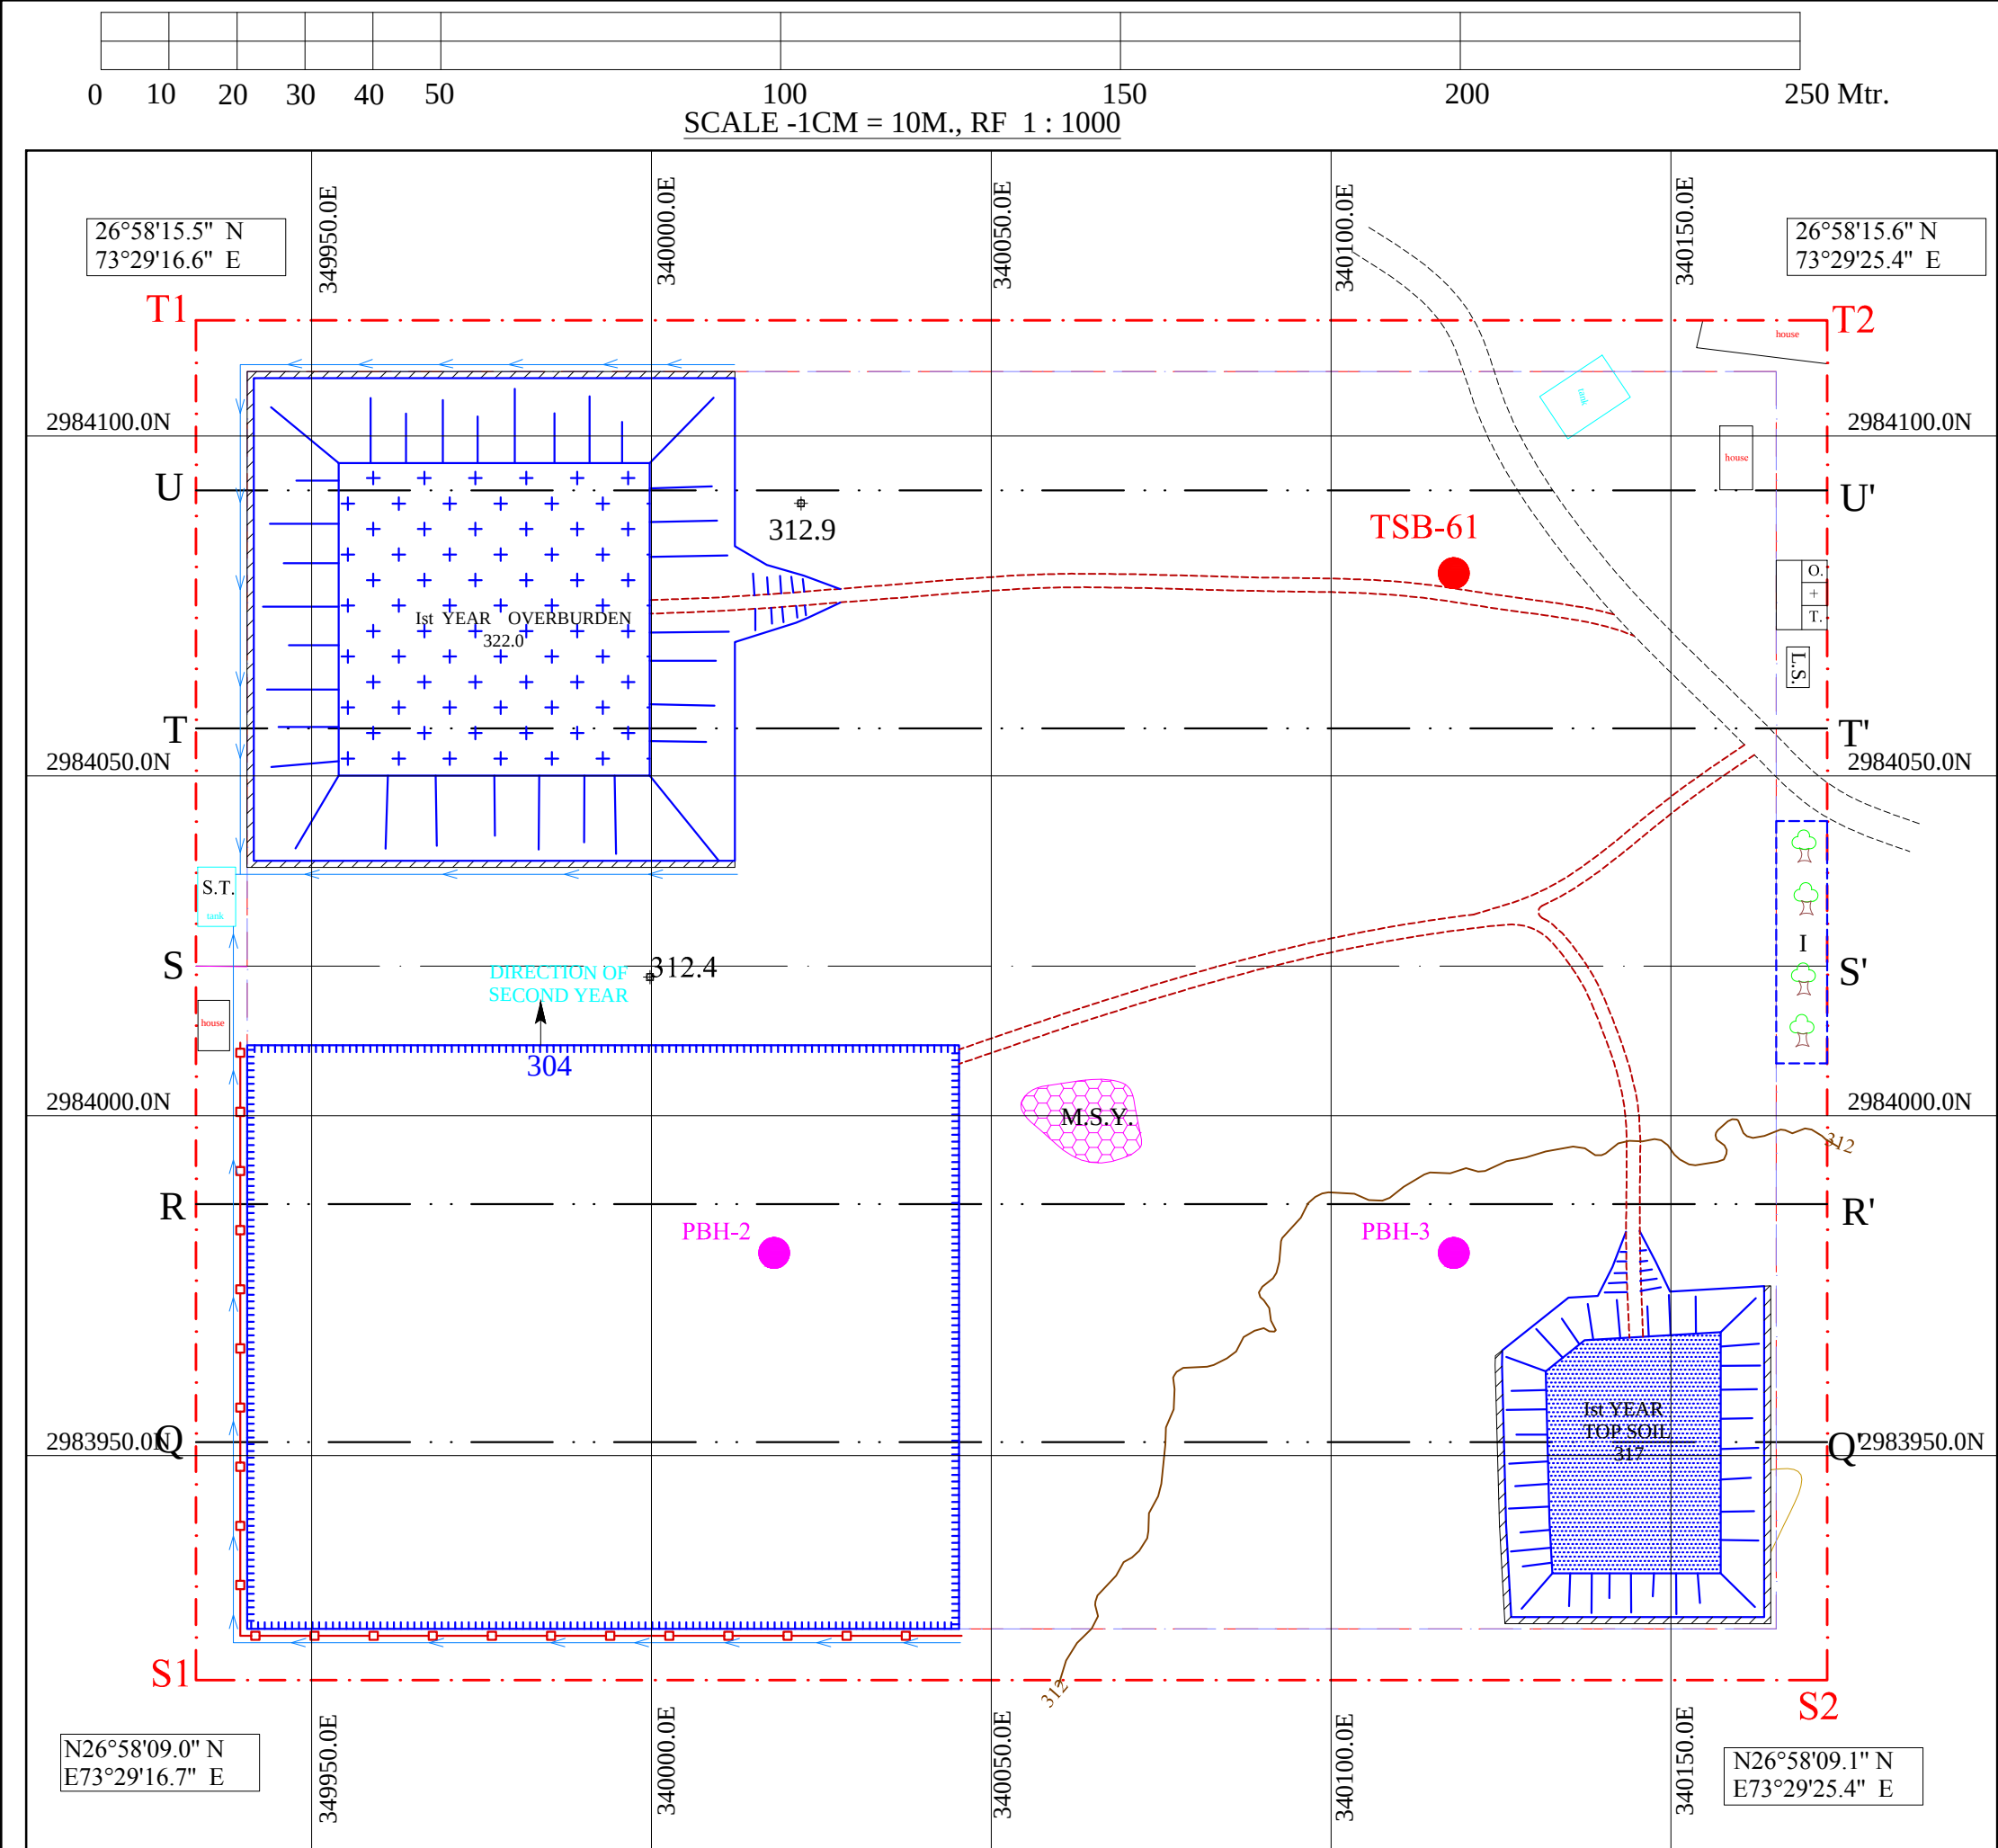

INDEX	
	BLOCK BOUNDARY
	7.5M. STATUTORY BARRIER
	CONTOUR
	GEO-COORDINATES (S2 Pillar)
	GRID LINE (UTM WGS 84)
	ROAD / RASTA
	SECTION LINE
	EXISTING INFRASTRUCTURE
	ULTIMATE PIT LIMIT
	PROP. MINERAL STACK YARD
	PROPOSED RETAINING WALL
	PROP. HAULAGE ROAD (1:16)
	PROPOSED 1st YEAR TOP SOIL STACK YARD
	PROP. 1st YEAR MINE WORKING
	PROPOSED 1st YEAR OVERBURDEN
	PROP. 1st YEAR PLANTATION
	PROP. GARLAND DRAIN
	PROPOSED SETTING TANK
	PROPOSED FENCING
	PROPOSED OFFICE COMPLEX
	PROPOSED LABOUR SHED
	EXISTING BORE HOLE
	PROPOSED BORE HOLE
	SPOT MRL


PROPOSED 1st YEAR DEVELOPMENT
PLAN OF HARIPURA LIMESTONE
BLOCK TKSB-18FOR AREA
OF 4.800 HECT.

N/v - Haripura, Tehsil -Kheenvsar , Distt.- **Nagaur** (Raj.)
Mineral - Limestone
Applicant - M/s. Suncity Chemical &
Minerals Private Limited
Area - 4.800 Hect. , Scale - 1 : 1000







PLATE NO.- 5A

THIS IS CERTIFIED THAT THE PLAN IS PREPARED BASED ON THE BLOCK MAP
AUTHENTICATED BY THE STATE GOVT. AND ARE CORRECT TO THE BEST OF MY KNOWLEDGE

QUALIFIED PERSON
MINING ENGINEER

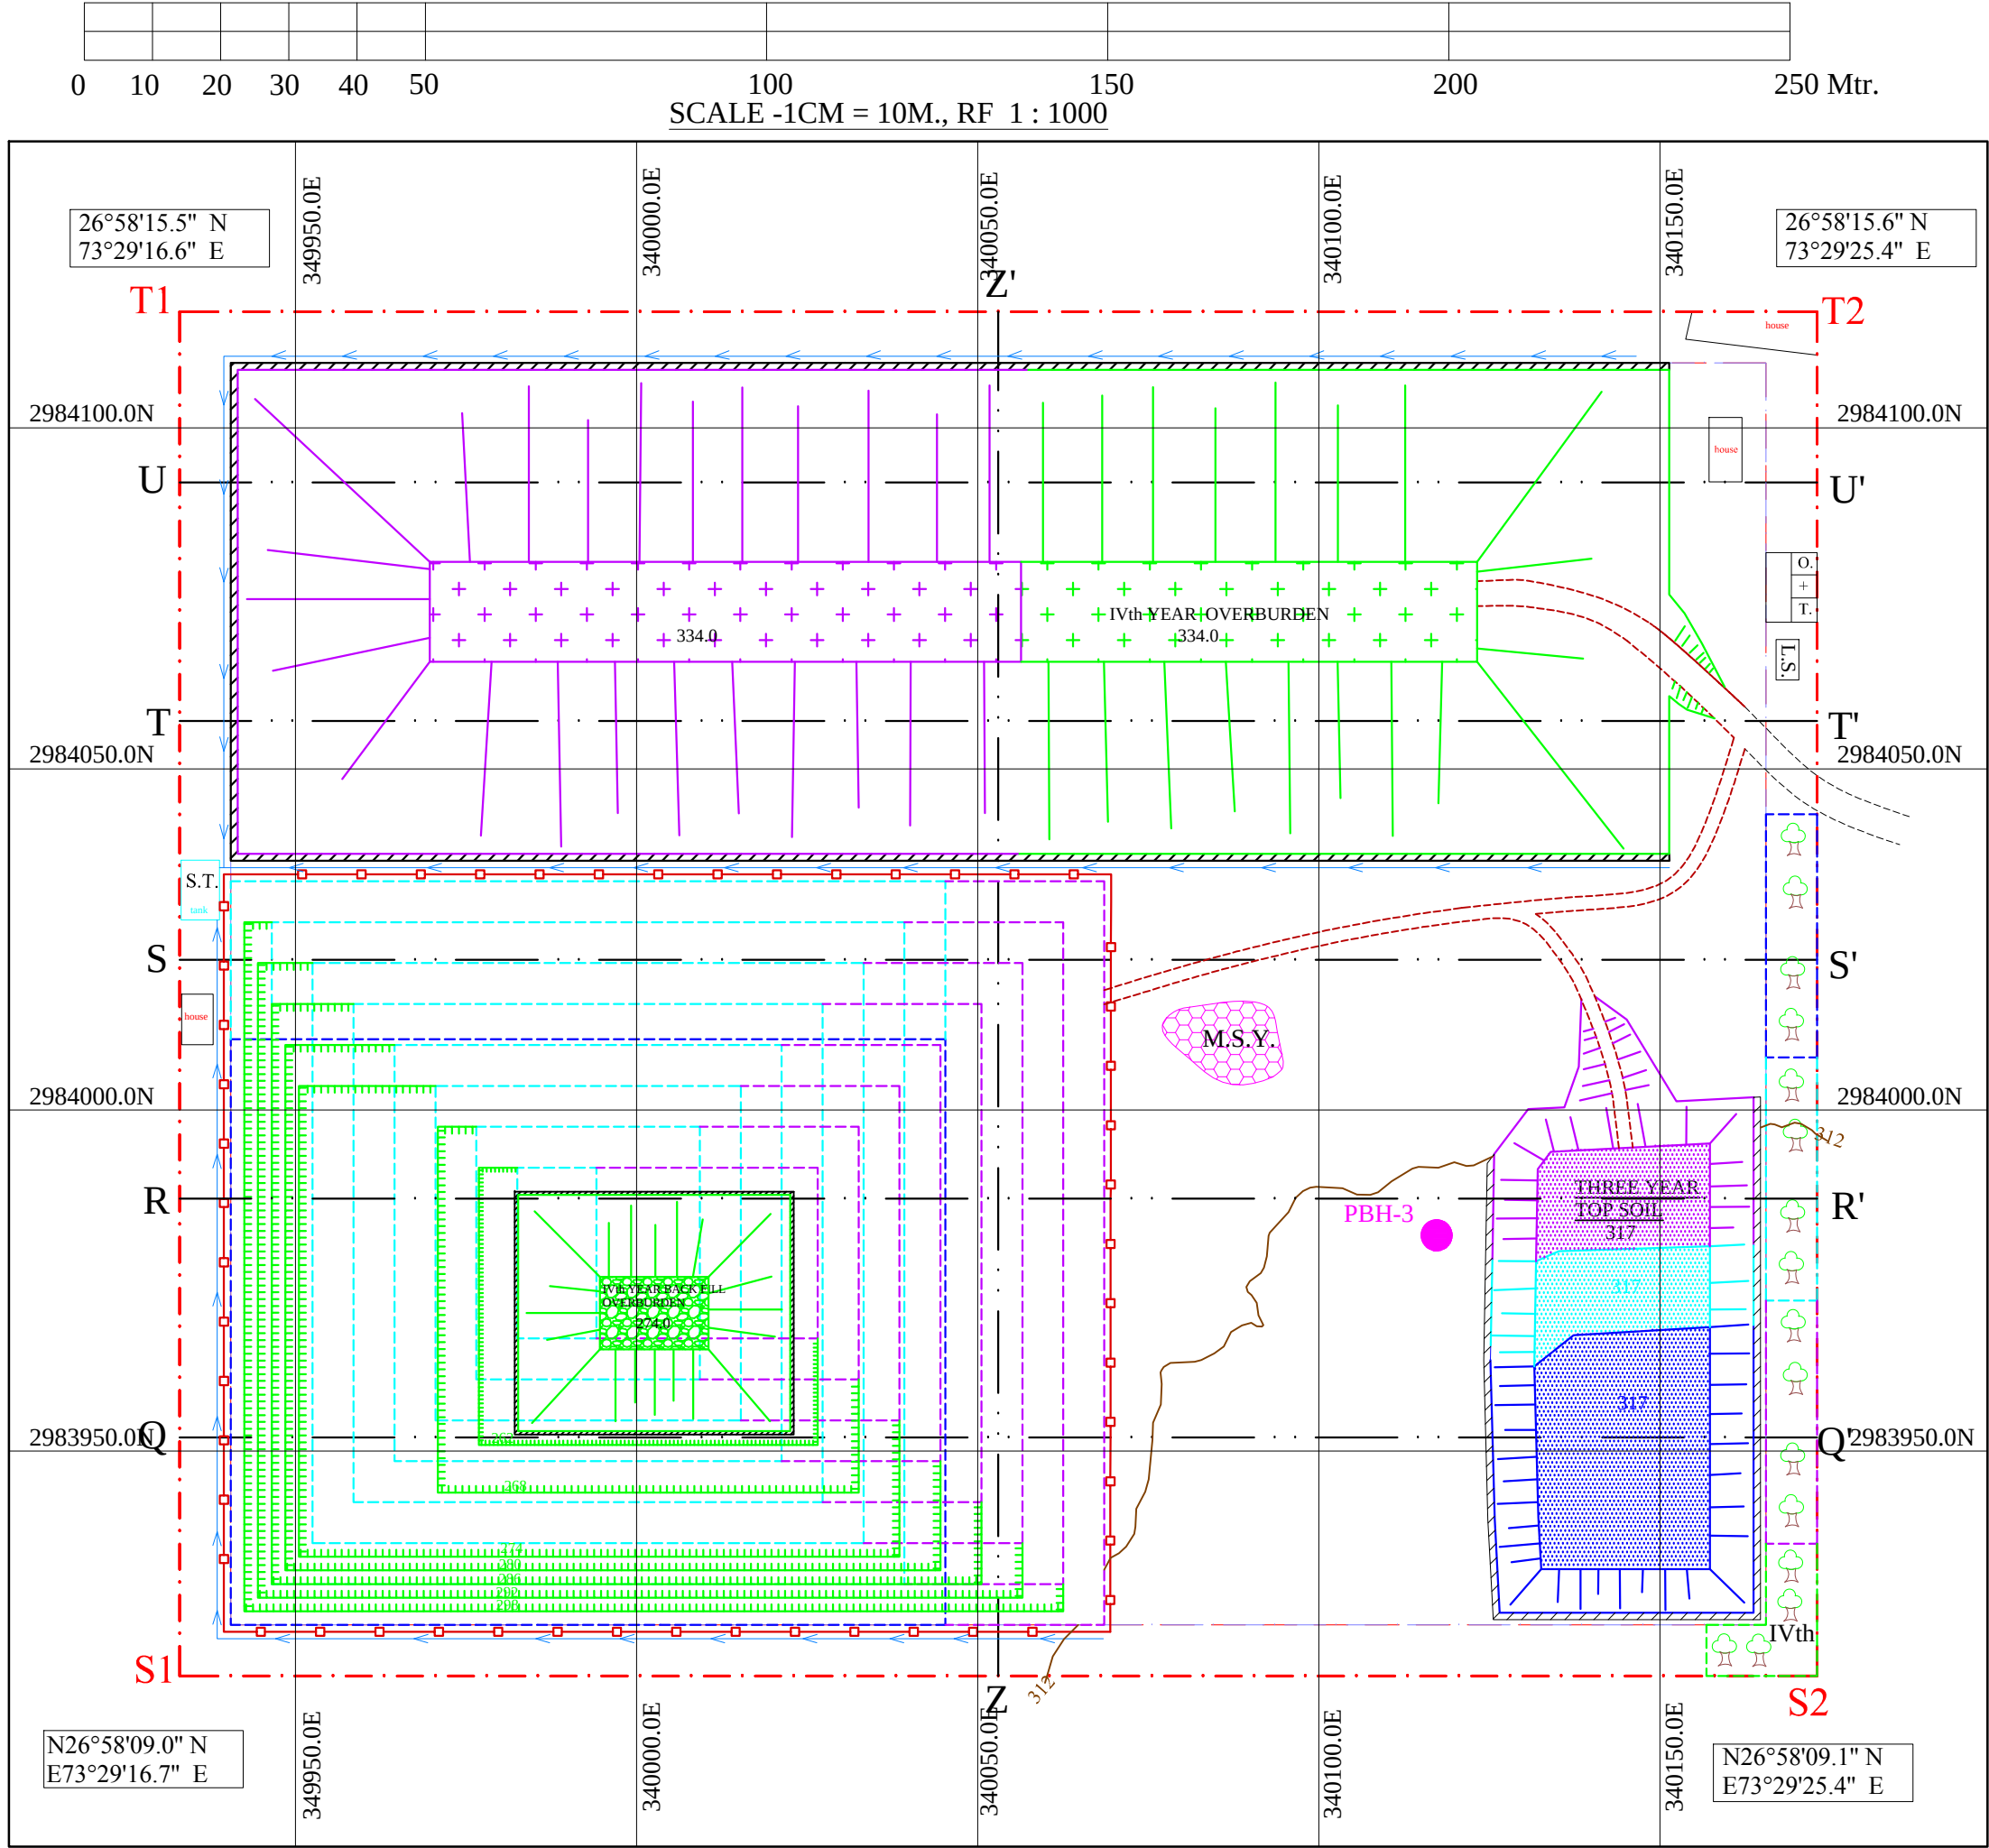

DRONE SURVEY DATE
10 . 03 . 2025

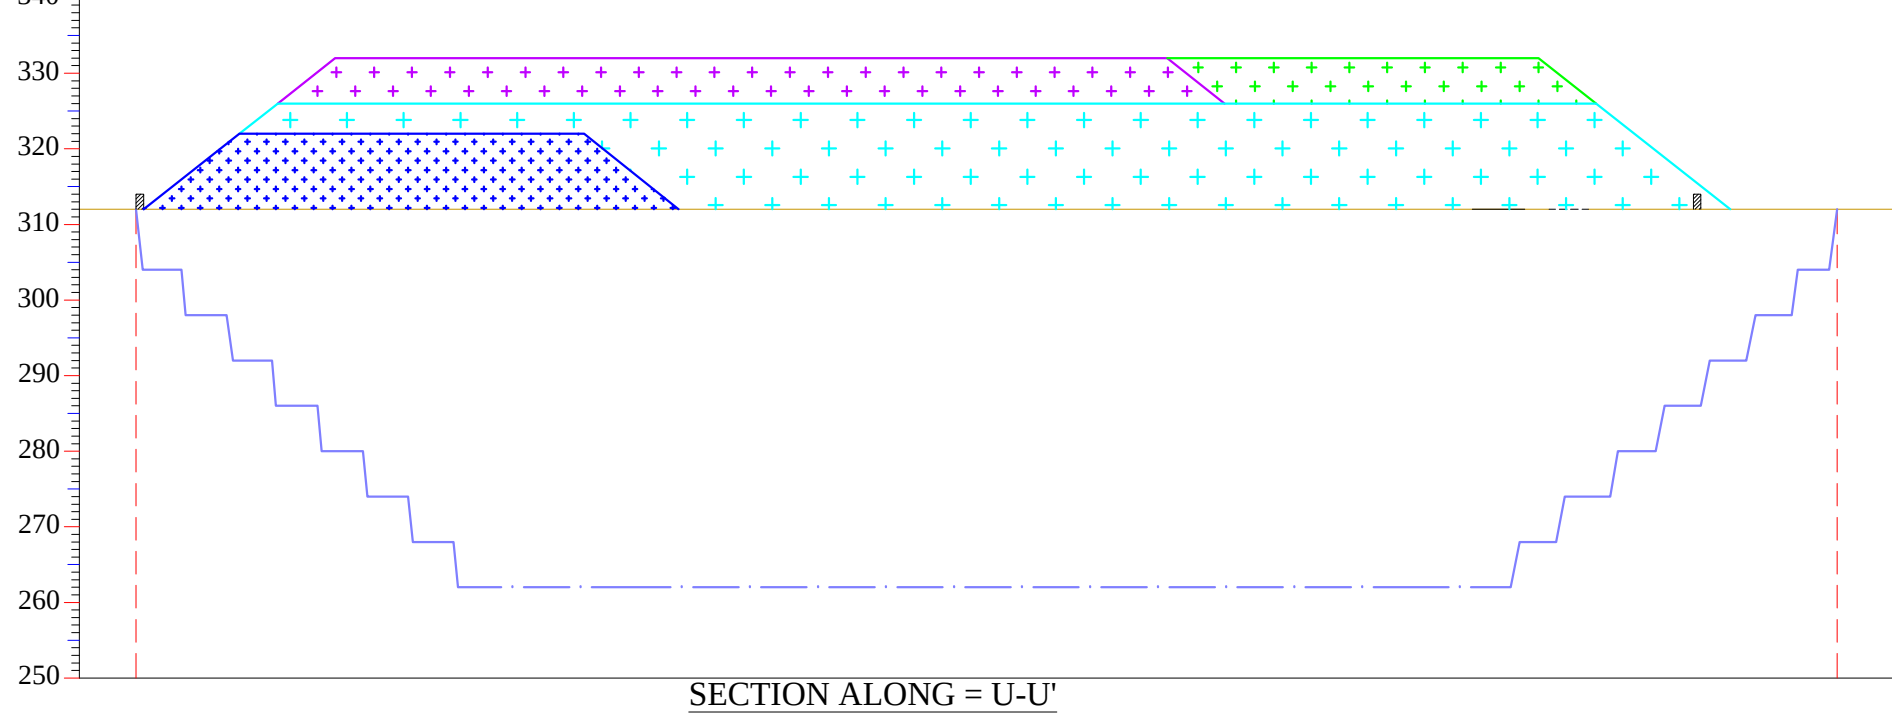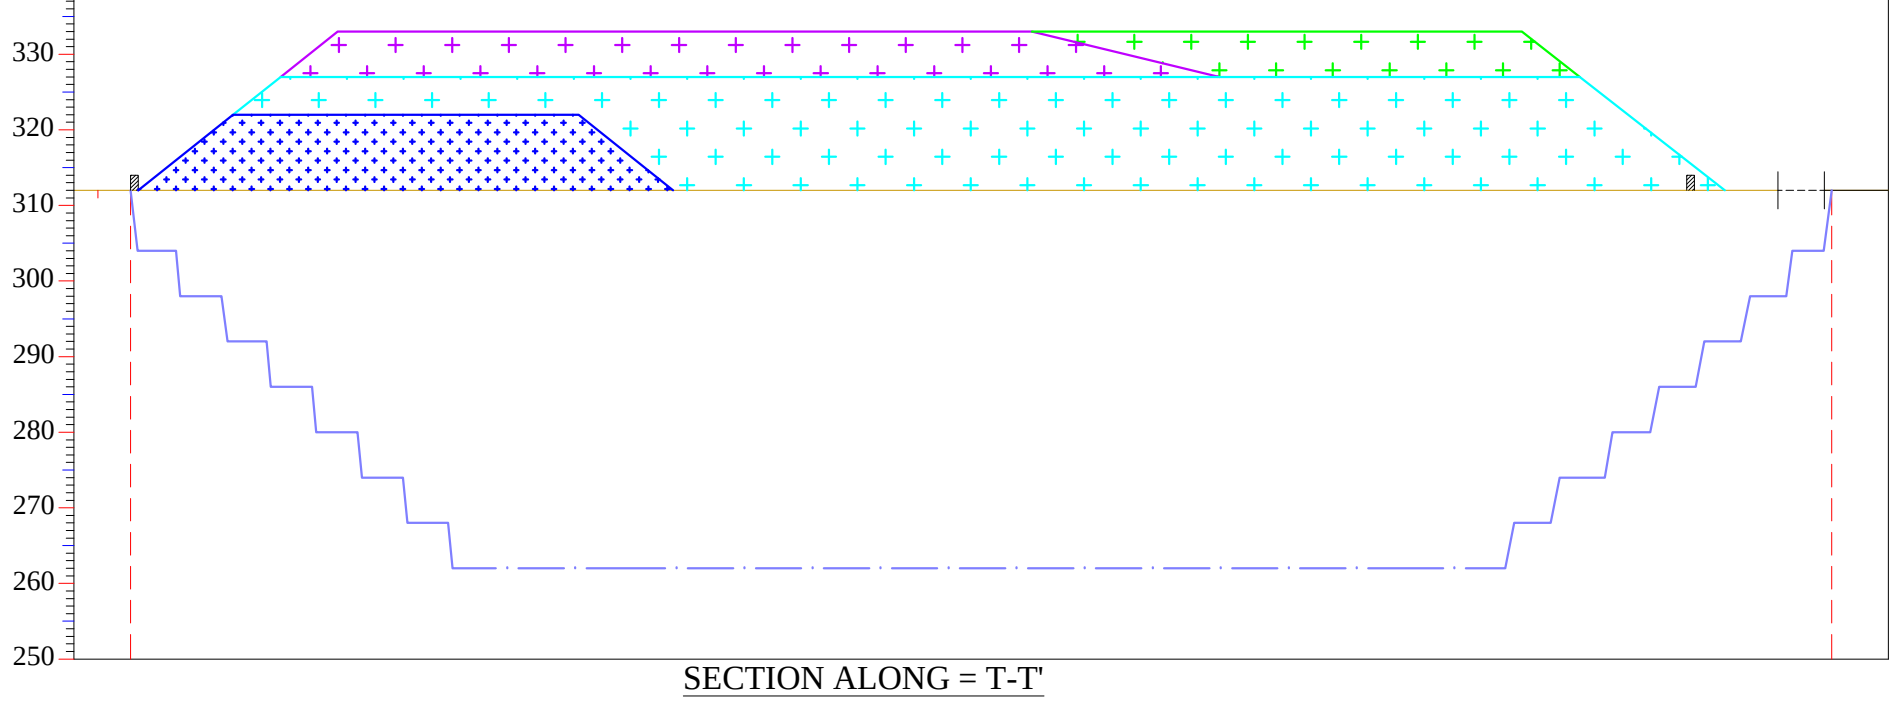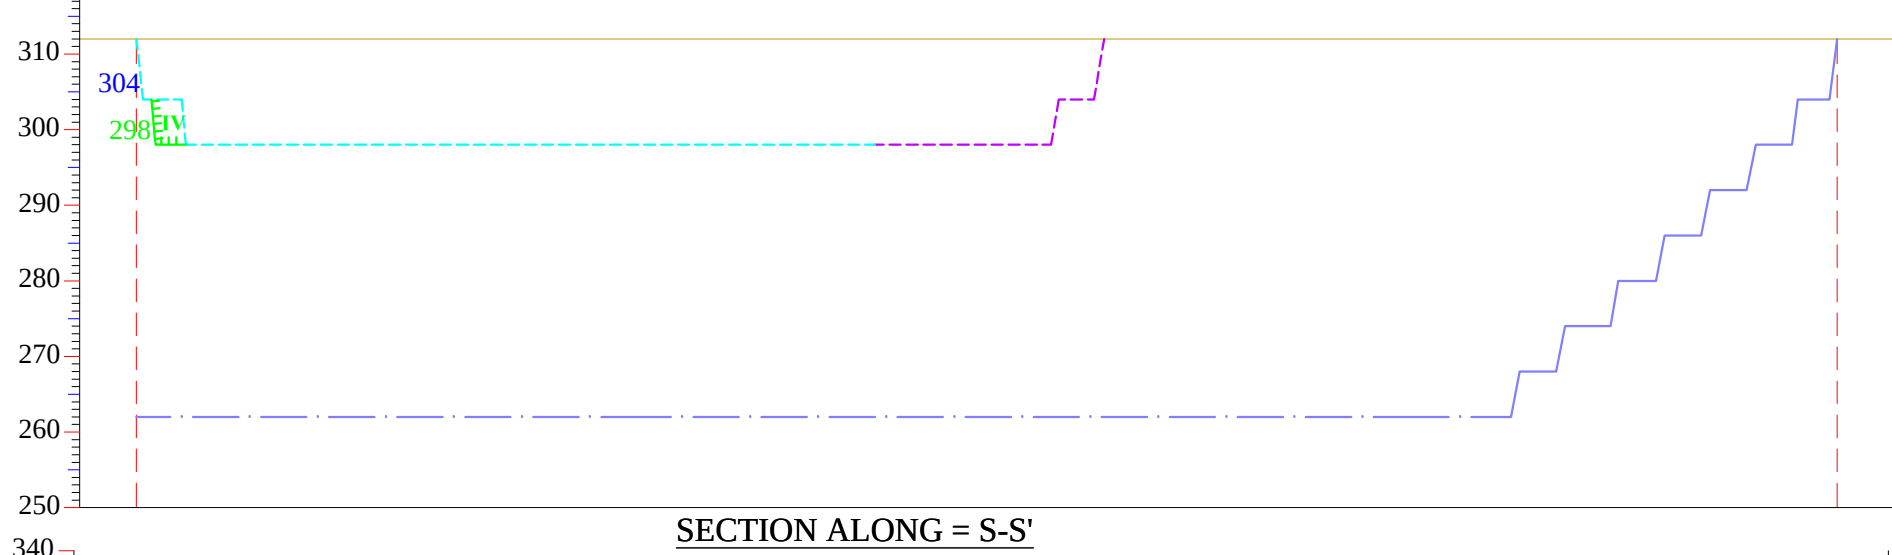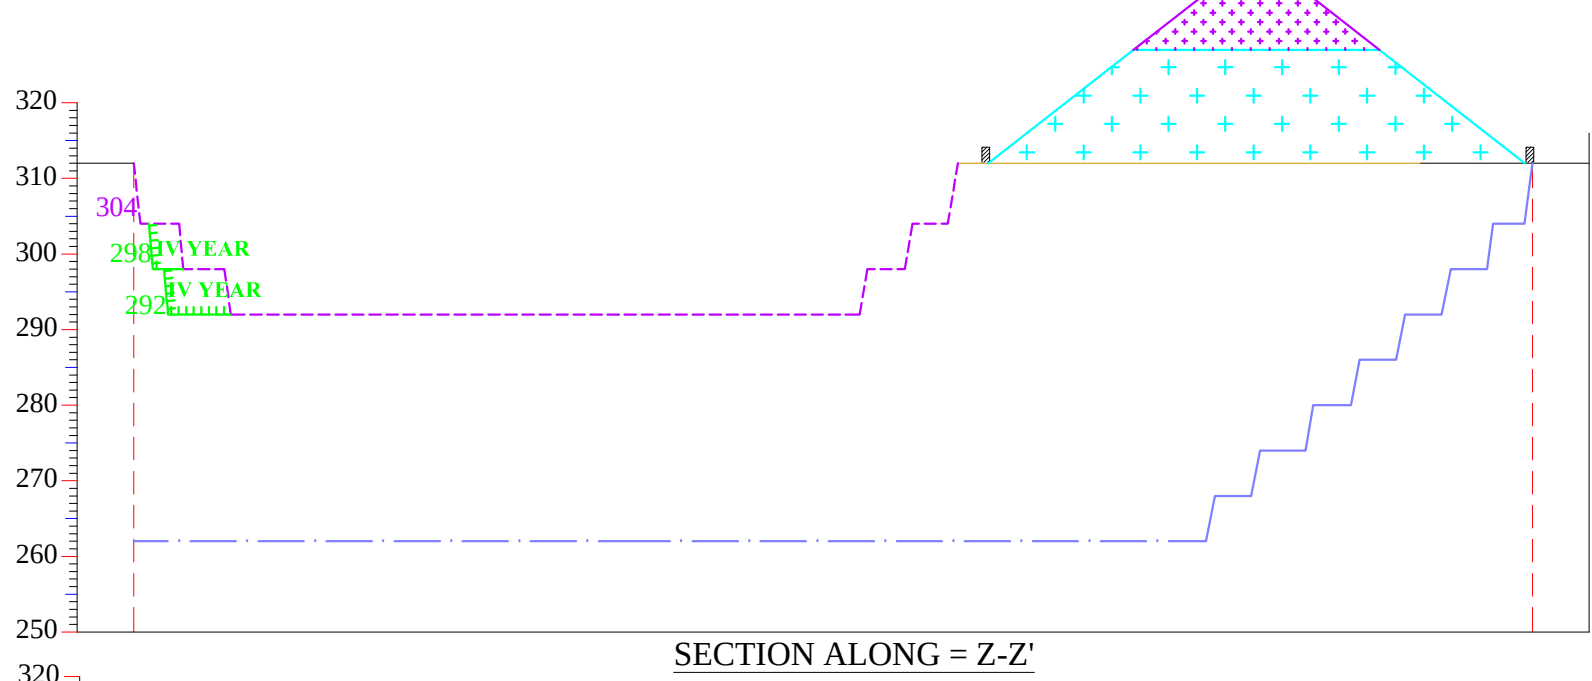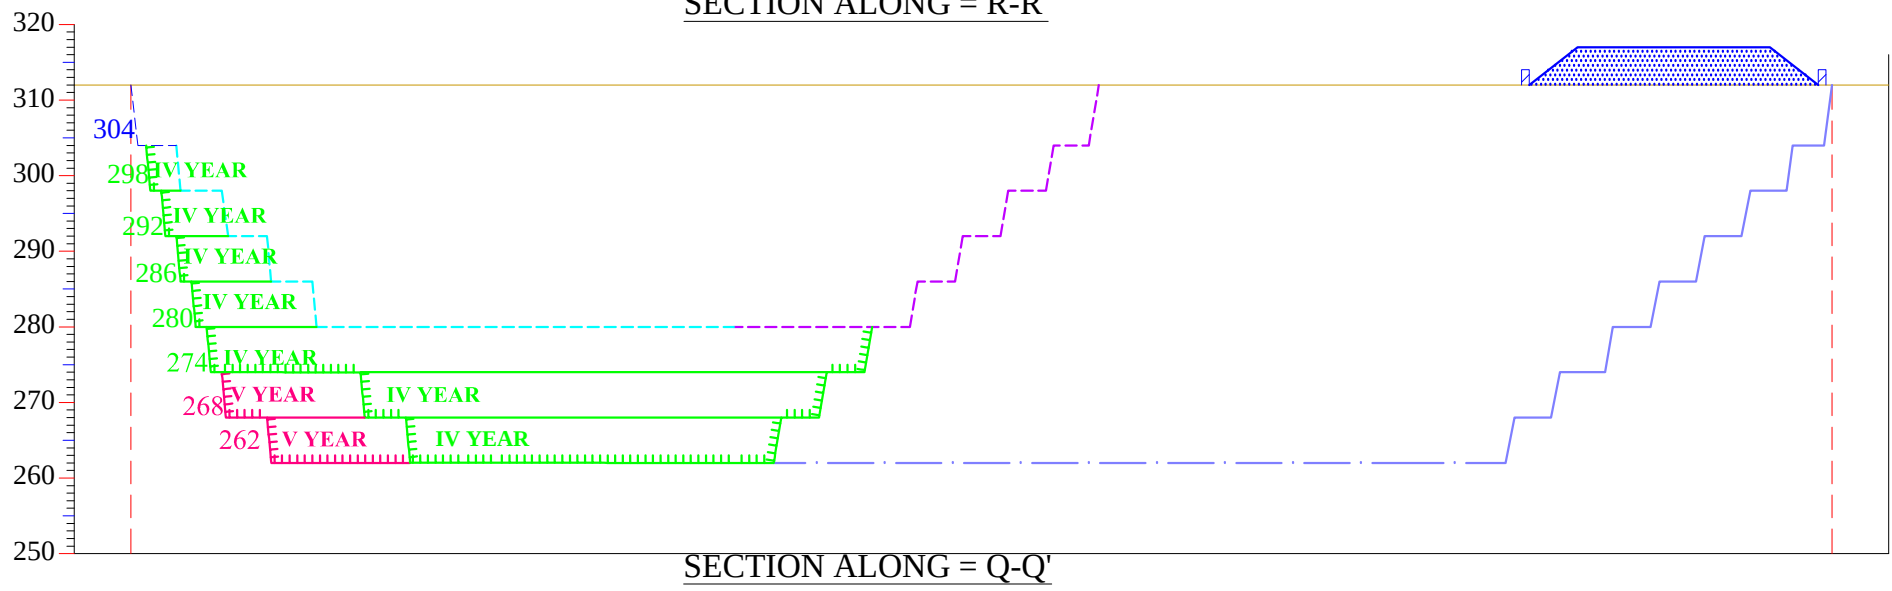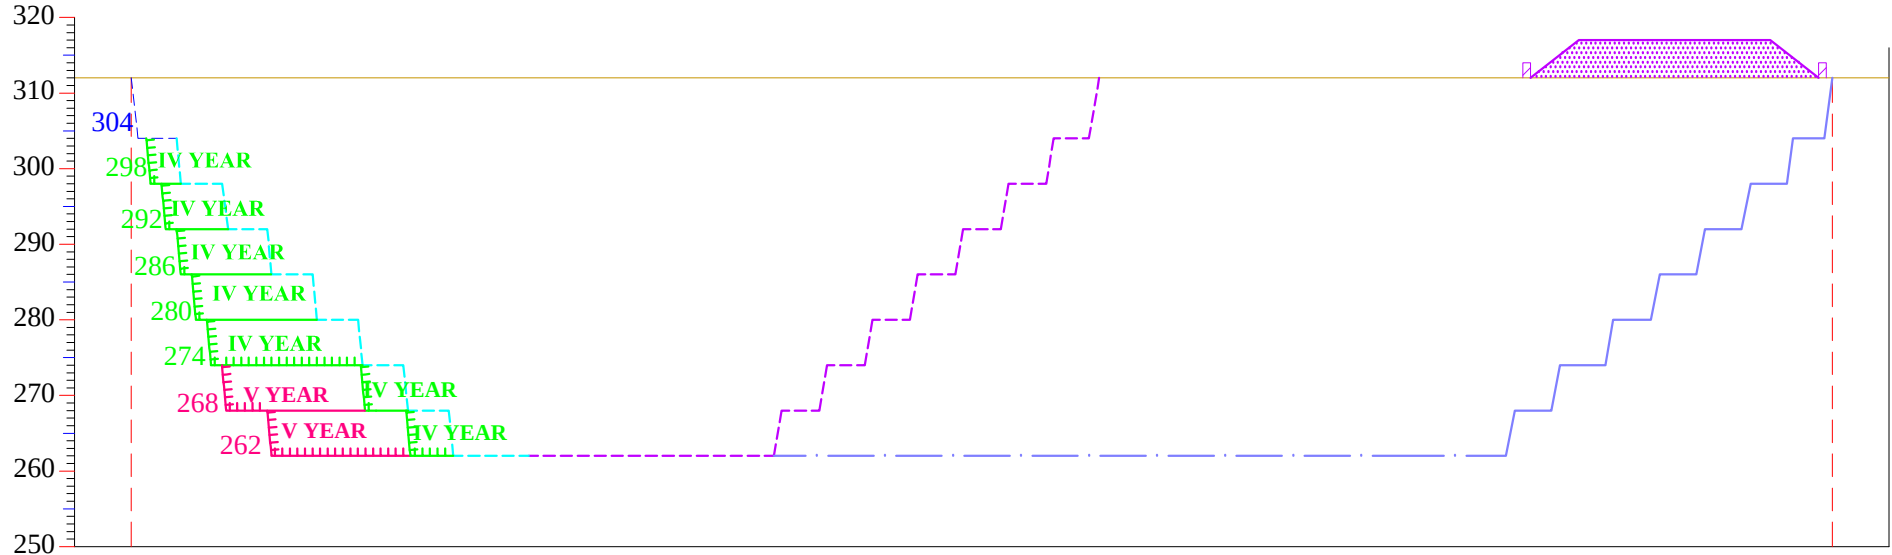

INDEX

	BLOCK BOUNDARY
	7.5M. STATUTORY BARRIER
	CONTOUR
	GEO-COORDINATES (S2 Pillar)
	GRID LINE (UTM WGS 84)
	ROAD / RASTA
	SECTION LINE
	EXISTING INFRASTRUCTURE
	ULTIMATE PIT LIMIT
	PROP. MINERAL STACK YARD
	PROPOSED RETAINING WALL
	PROP. HAULAGE ROAD (1:16)
	PROP. THREE YEAR TOP SOIL STACK YARD
	PROP. IVth YEAR MINE WORKING
	PROPOSED IVth YEAR OVERBURDEN
	PROPOSED IVth BACK FILL OVERBURDEN
	PROP. IVth YEAR PLANTATION
	PROP. GARLAND DRAIN
	PROPOSED SETTING TANK
	PROPOSED FENCING
	PROPOSED OFFICE COMPLEX
	PROPOSED LABOUR SHED
	PROPOSED BORE HOLE


PROPOSED IVth YEAR DEVELOPMENT
PLAN OF HARIPURA LIMESTONE
BLOCK TKSB-18FOR AREA
OF 4.800 HECT.

N/w - Haripura, Tehsil -Kheenvsar , Distt.- **Nagaur** (Raj.)
Mineral - Limestone
Applicant - M/s. Suncity Chemical &
Minerals Private Limited
Area - 4.800 Hect. , Scale - 1 : 1000

PLATE NO.- 5D

THIS IS CERTIFIED THAT THE PLAN IS PREPARED BASED ON THE BLOCK MAP
AUTHENTICATED BY THE STATE GOVT. AND ARE CORRECT TO THE BEST OF MY KNOWLEDGE


QUALIFIED PERSON
MINING ENGINEER

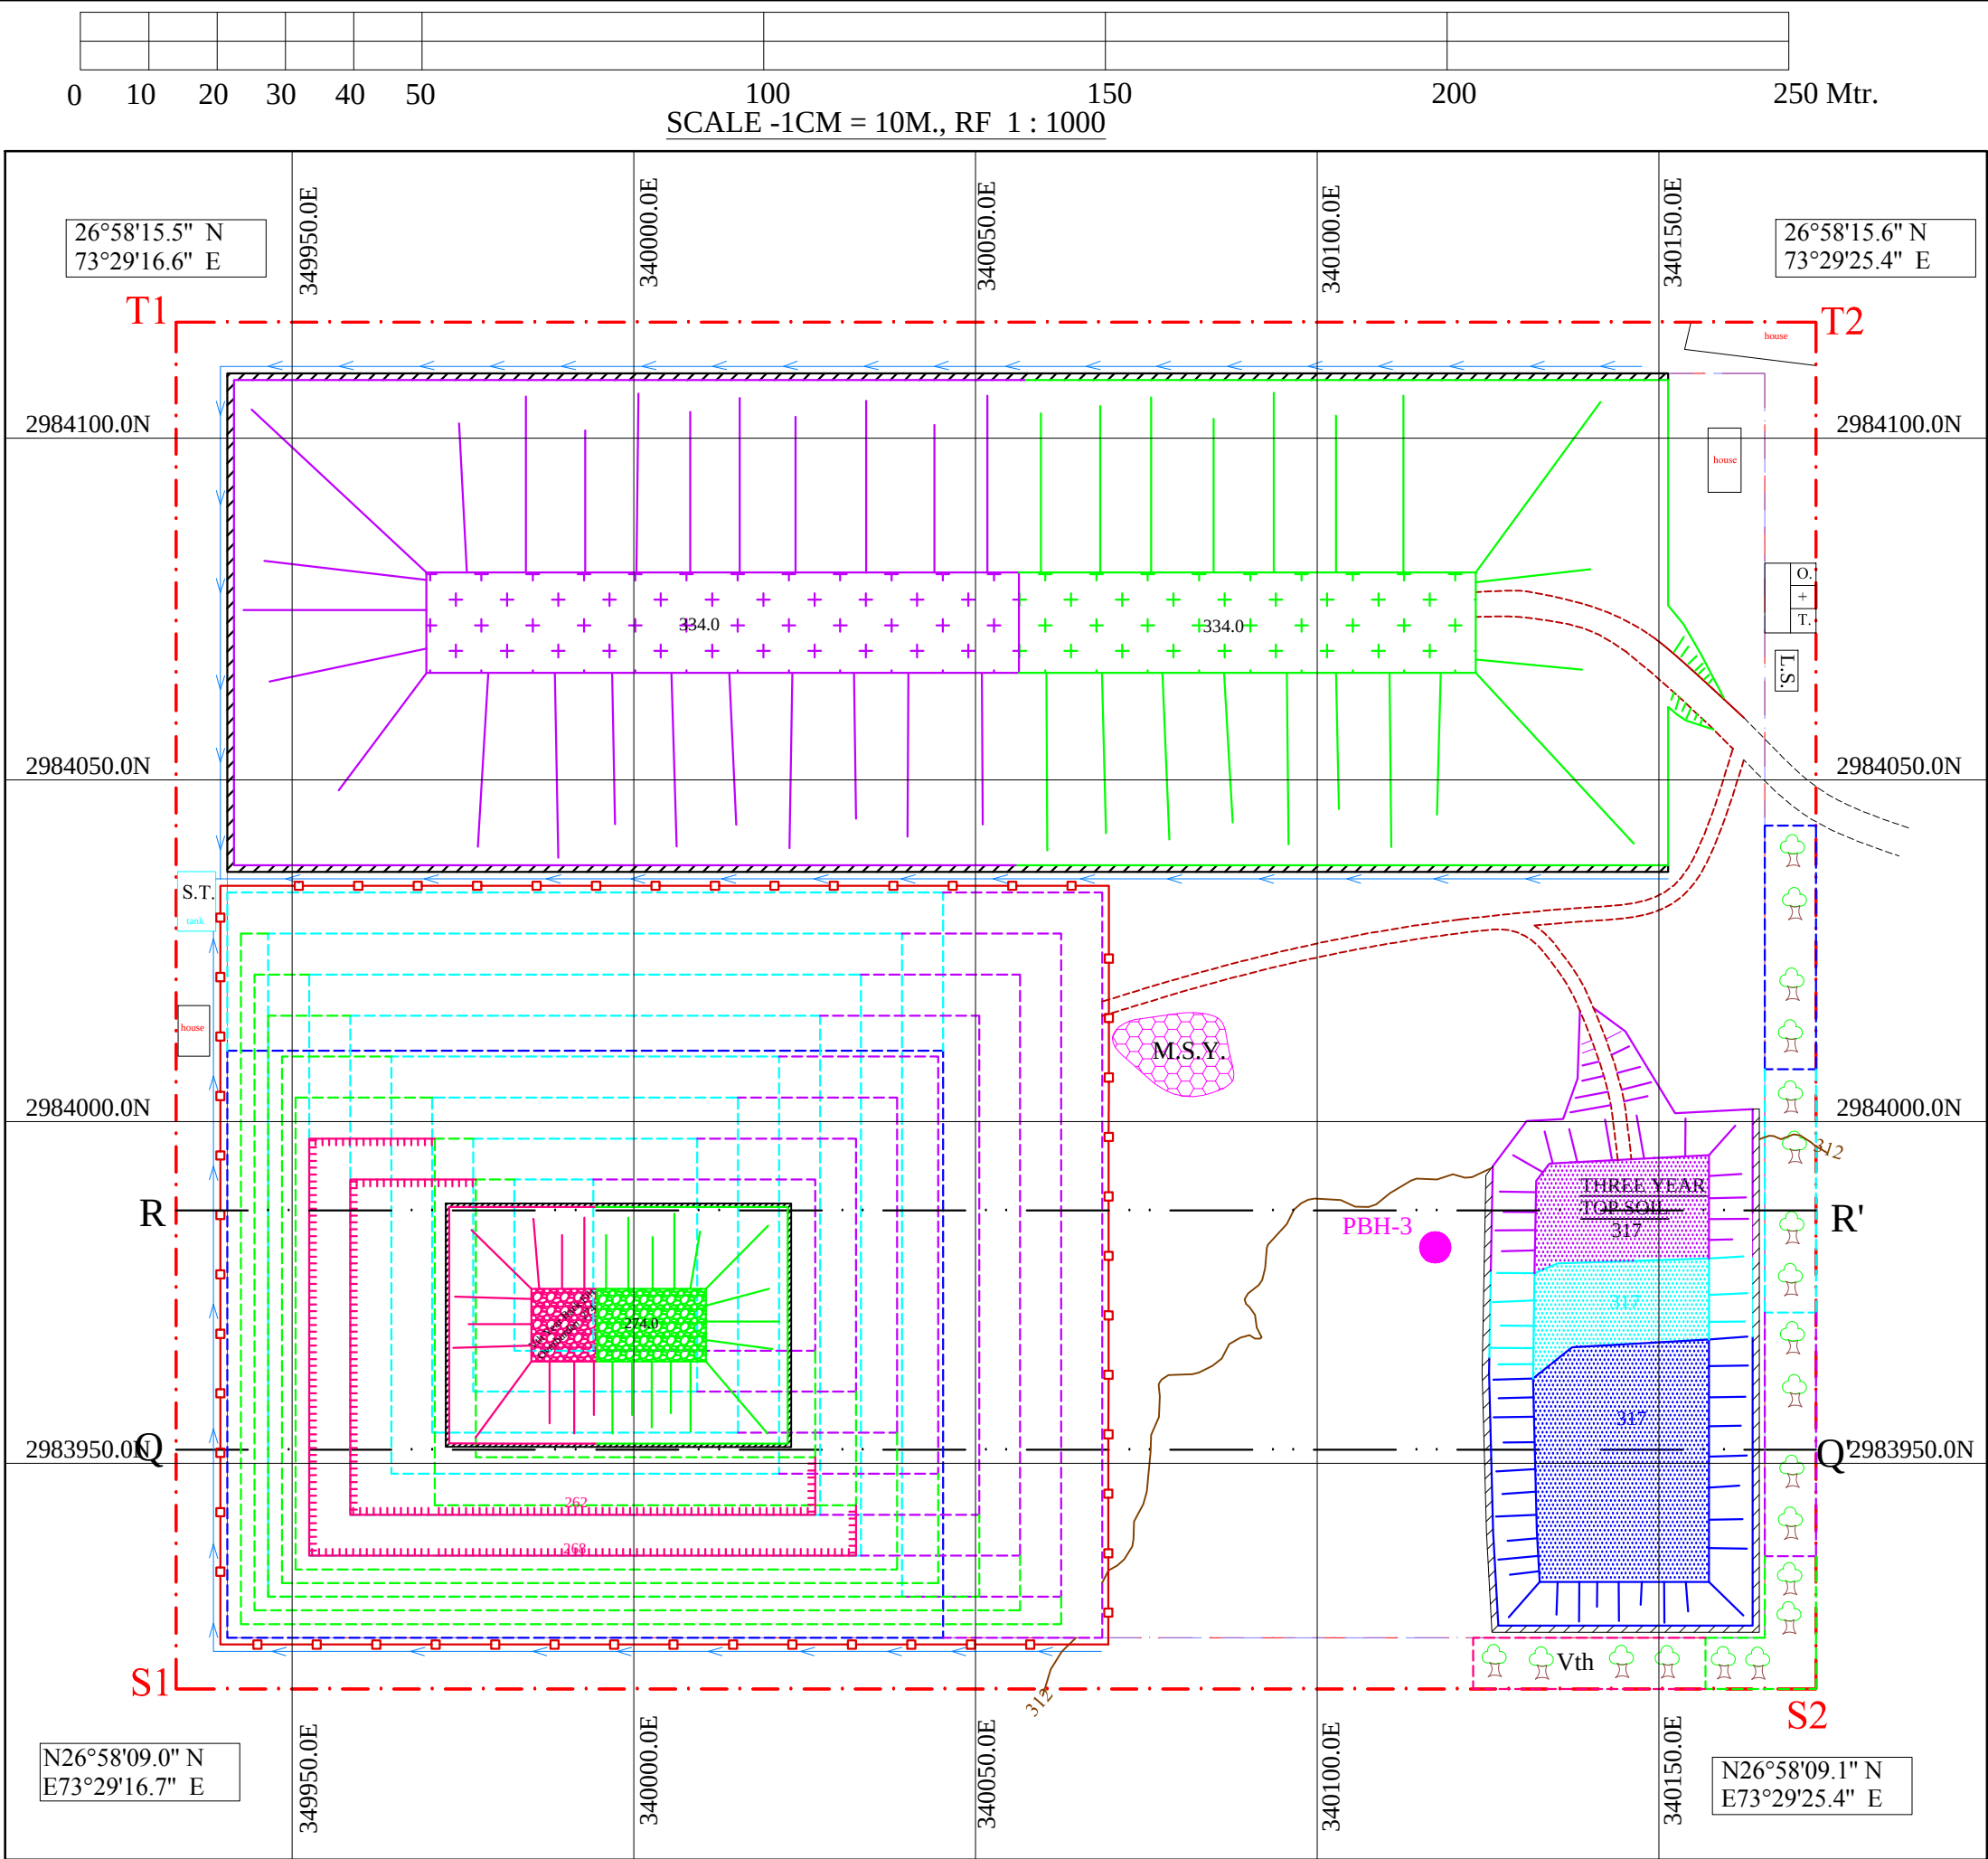


DRONE SURVEY DATE
10 . 03 . 2025

INDEX

	BLOCK BOUNDARY
	7.5M. STATUTORY BARRIER
	CONTOUR
	GEO-COORDINATES (S2 Pillar)
	GRID LINE (UTM WGS 84)
	ROAD / RASTA
	SECTION LINE
	EXISTING INFRASTRUCTURE
	ULTIMATE PIT LIMIT
	PROP. MINERAL STACK YARD
	PROPOSED RETAINING WALL
	PROP. HAULAGE ROAD (1:16)
	PROP. THREE YEAR TOP SOIL STACK YARD
	PROP. Vth YEAR MINE WORKING
	PROPOSED Vth BACK FILL OVERBURDEN
	PROP. Vth YEAR PLANTATION
	PROP. GARLAND DRAIN
	PROPOSED SETTING TANK
	PROPOSED FENCING
	PROPOSED OFFICE COMPLEX
	PROPOSED LABOUR SHED
	PROPOSED BORE HOLE

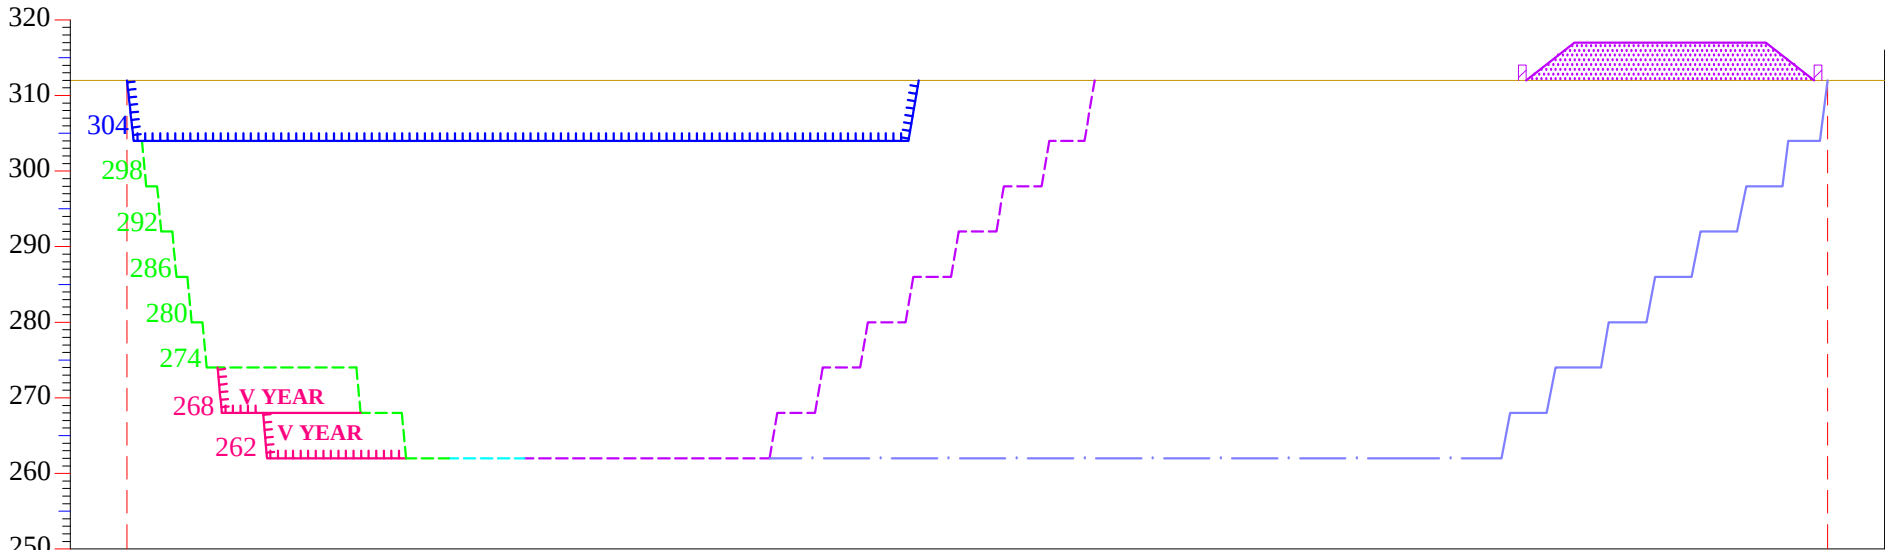

SECTION ALONG = R-R'

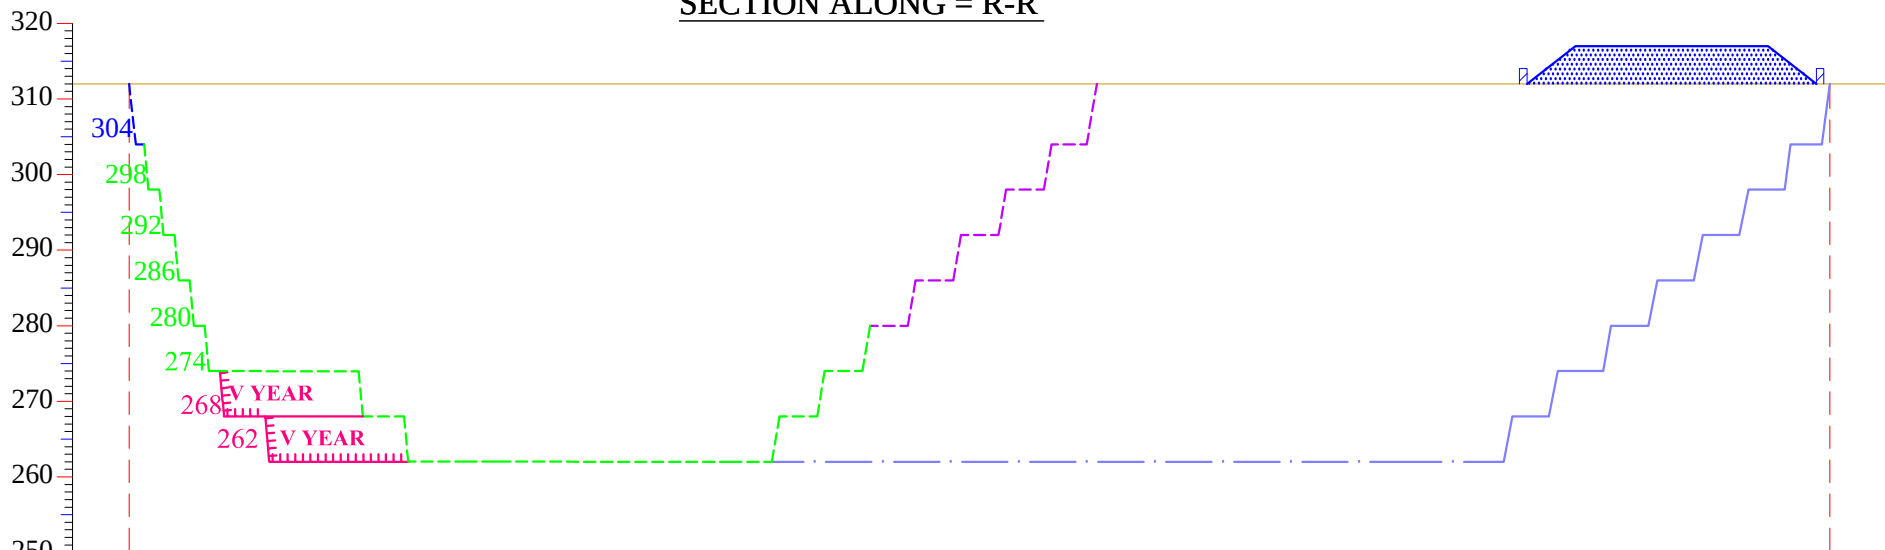

SECTION ALONG = Q-Q'

PROPOSED Vth YEAR DEVELOPMENT
PLAN OF HARIPURA LIMESTONE
BLOCK TKSB-18FOR AREA
OF 4.800 HECT.

N\ v - Haripura, Tehsil -Kheenvsar , Distt.- **Nagaur** (Raj.)
Mineral - Limestone
Applicant - M/s. Suncity Chemical &
Minerals Private Limited
Area - 4.800 Hect. , Scale - 1 : 1000

PLATE NO.- 5E

THIS IS CERTIFIED THAT THE PLAN IS PREPARED BASED ON THE BLOCK MAP
AUTHENTICATED BY THE STATE GOVT. AND ARE CORRECT TO THE BEST OF MY KNOWLEDGE

QUALIFIED PERSON
MINING ENGINEER