
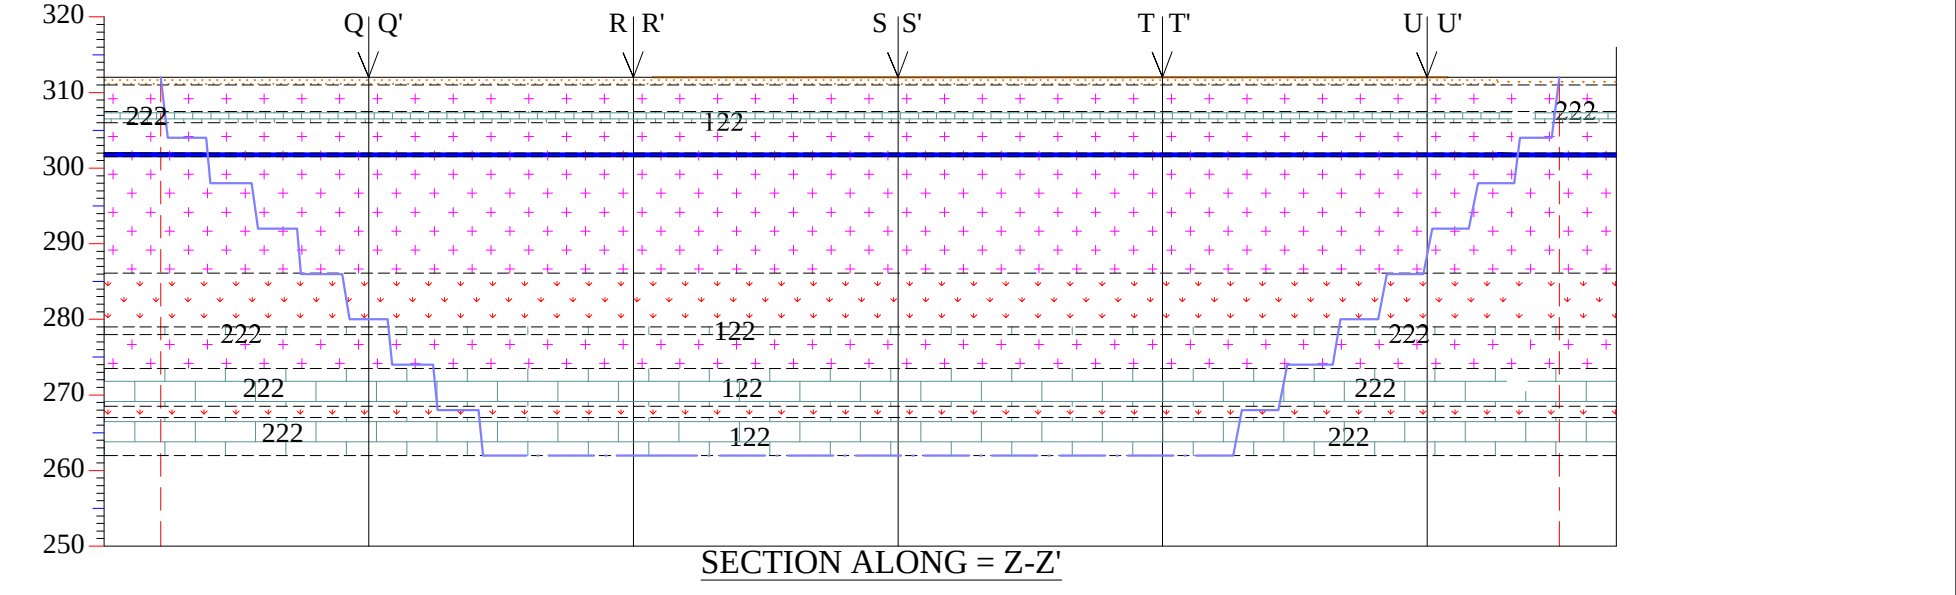
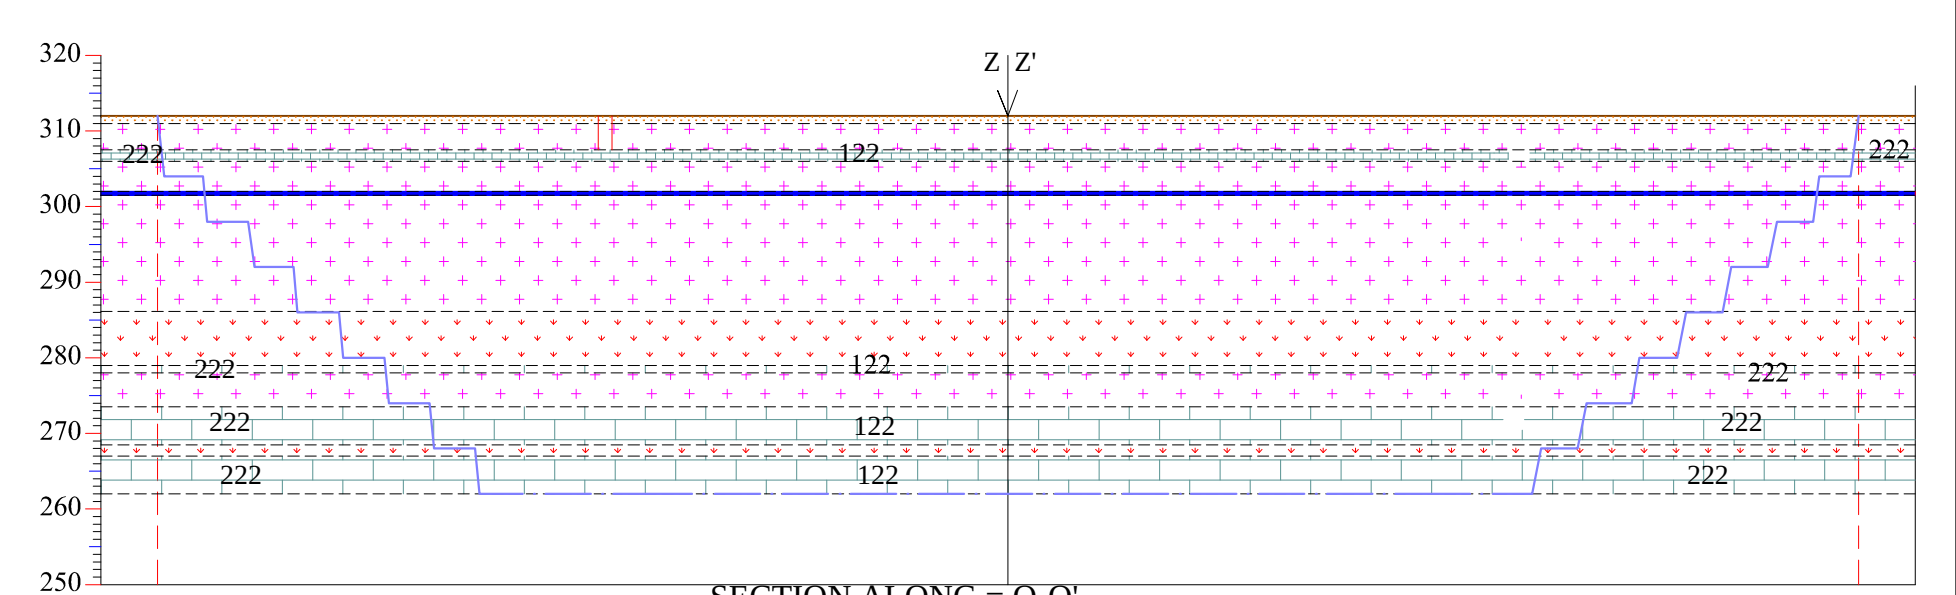


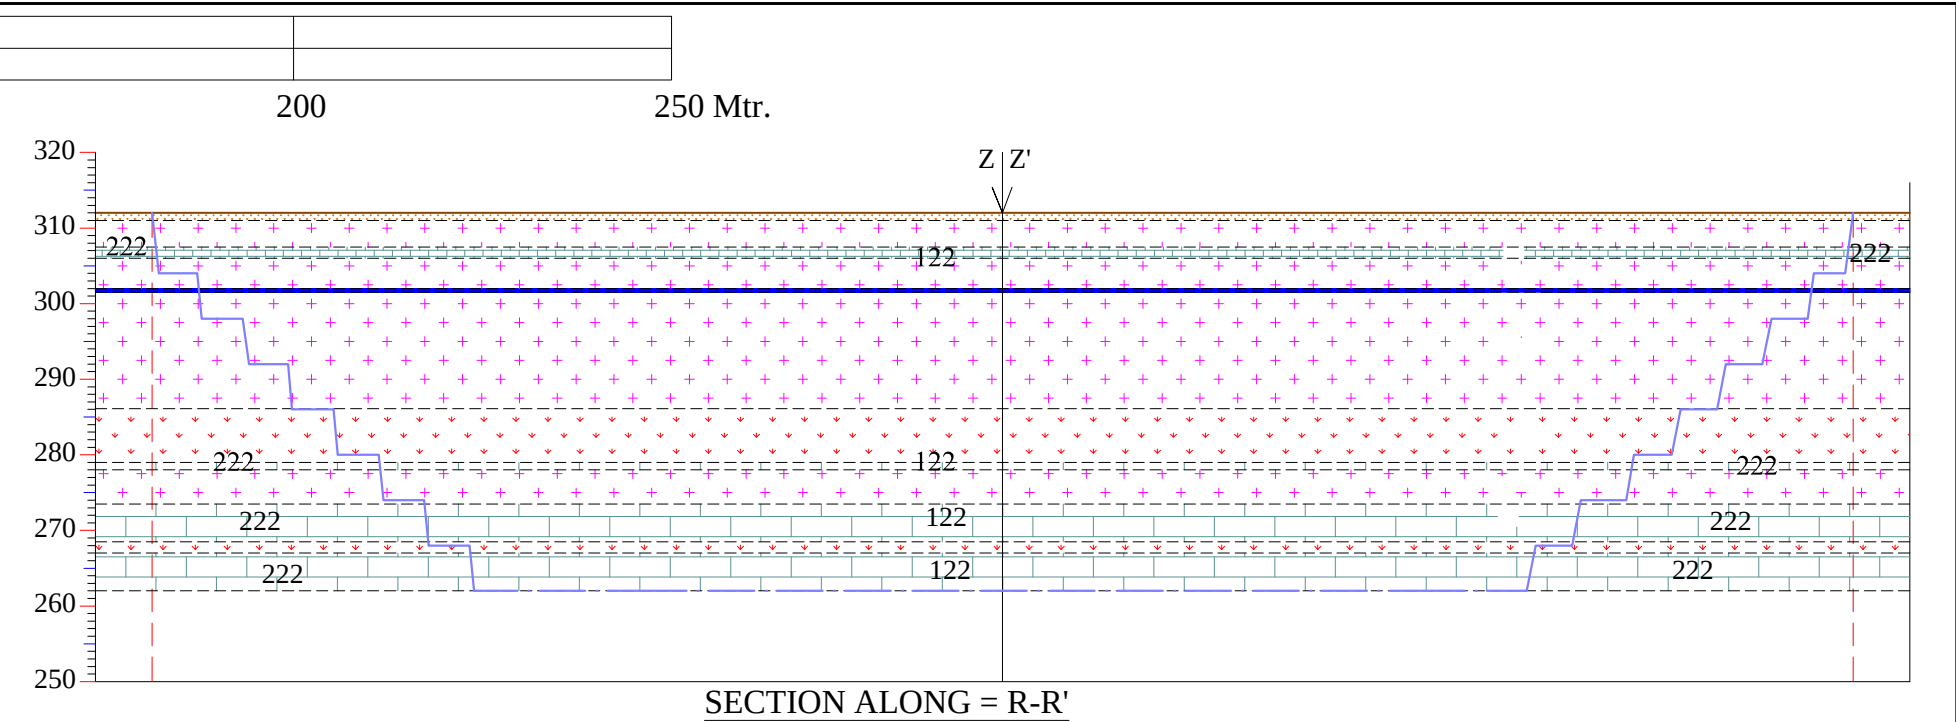

INDEX	
	LEASE BOUNDARY
	7.5M. STATUTORY BARRIER
	ULTIMATE PIT LIMIT
	MINE ROAD

N/v - Haripura, Tehsil -Kheenvsar , Distt.- **Nagaur** (Raj.)
Mineral - Limestone
Applicant - M/s. Suncity Chemical &
Minerals Private Limited
Area - 4.800 Hect. , Scale - 1 : 1000

Nimish Singhwi Digitally signed by
Nimish Singhwi Date: 2025.06.12
12:03:33 -07'00'

QUALIFIED PERSON
MINING ENGINEER