


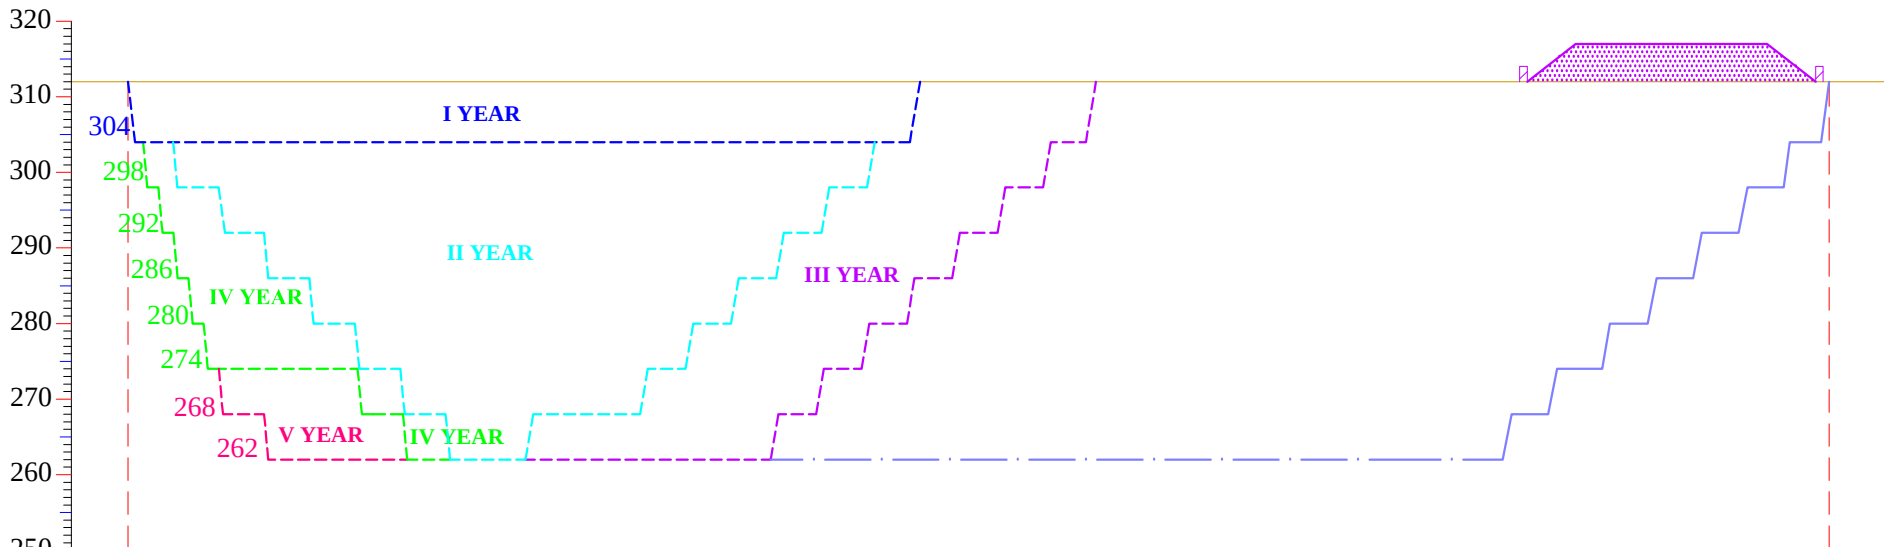


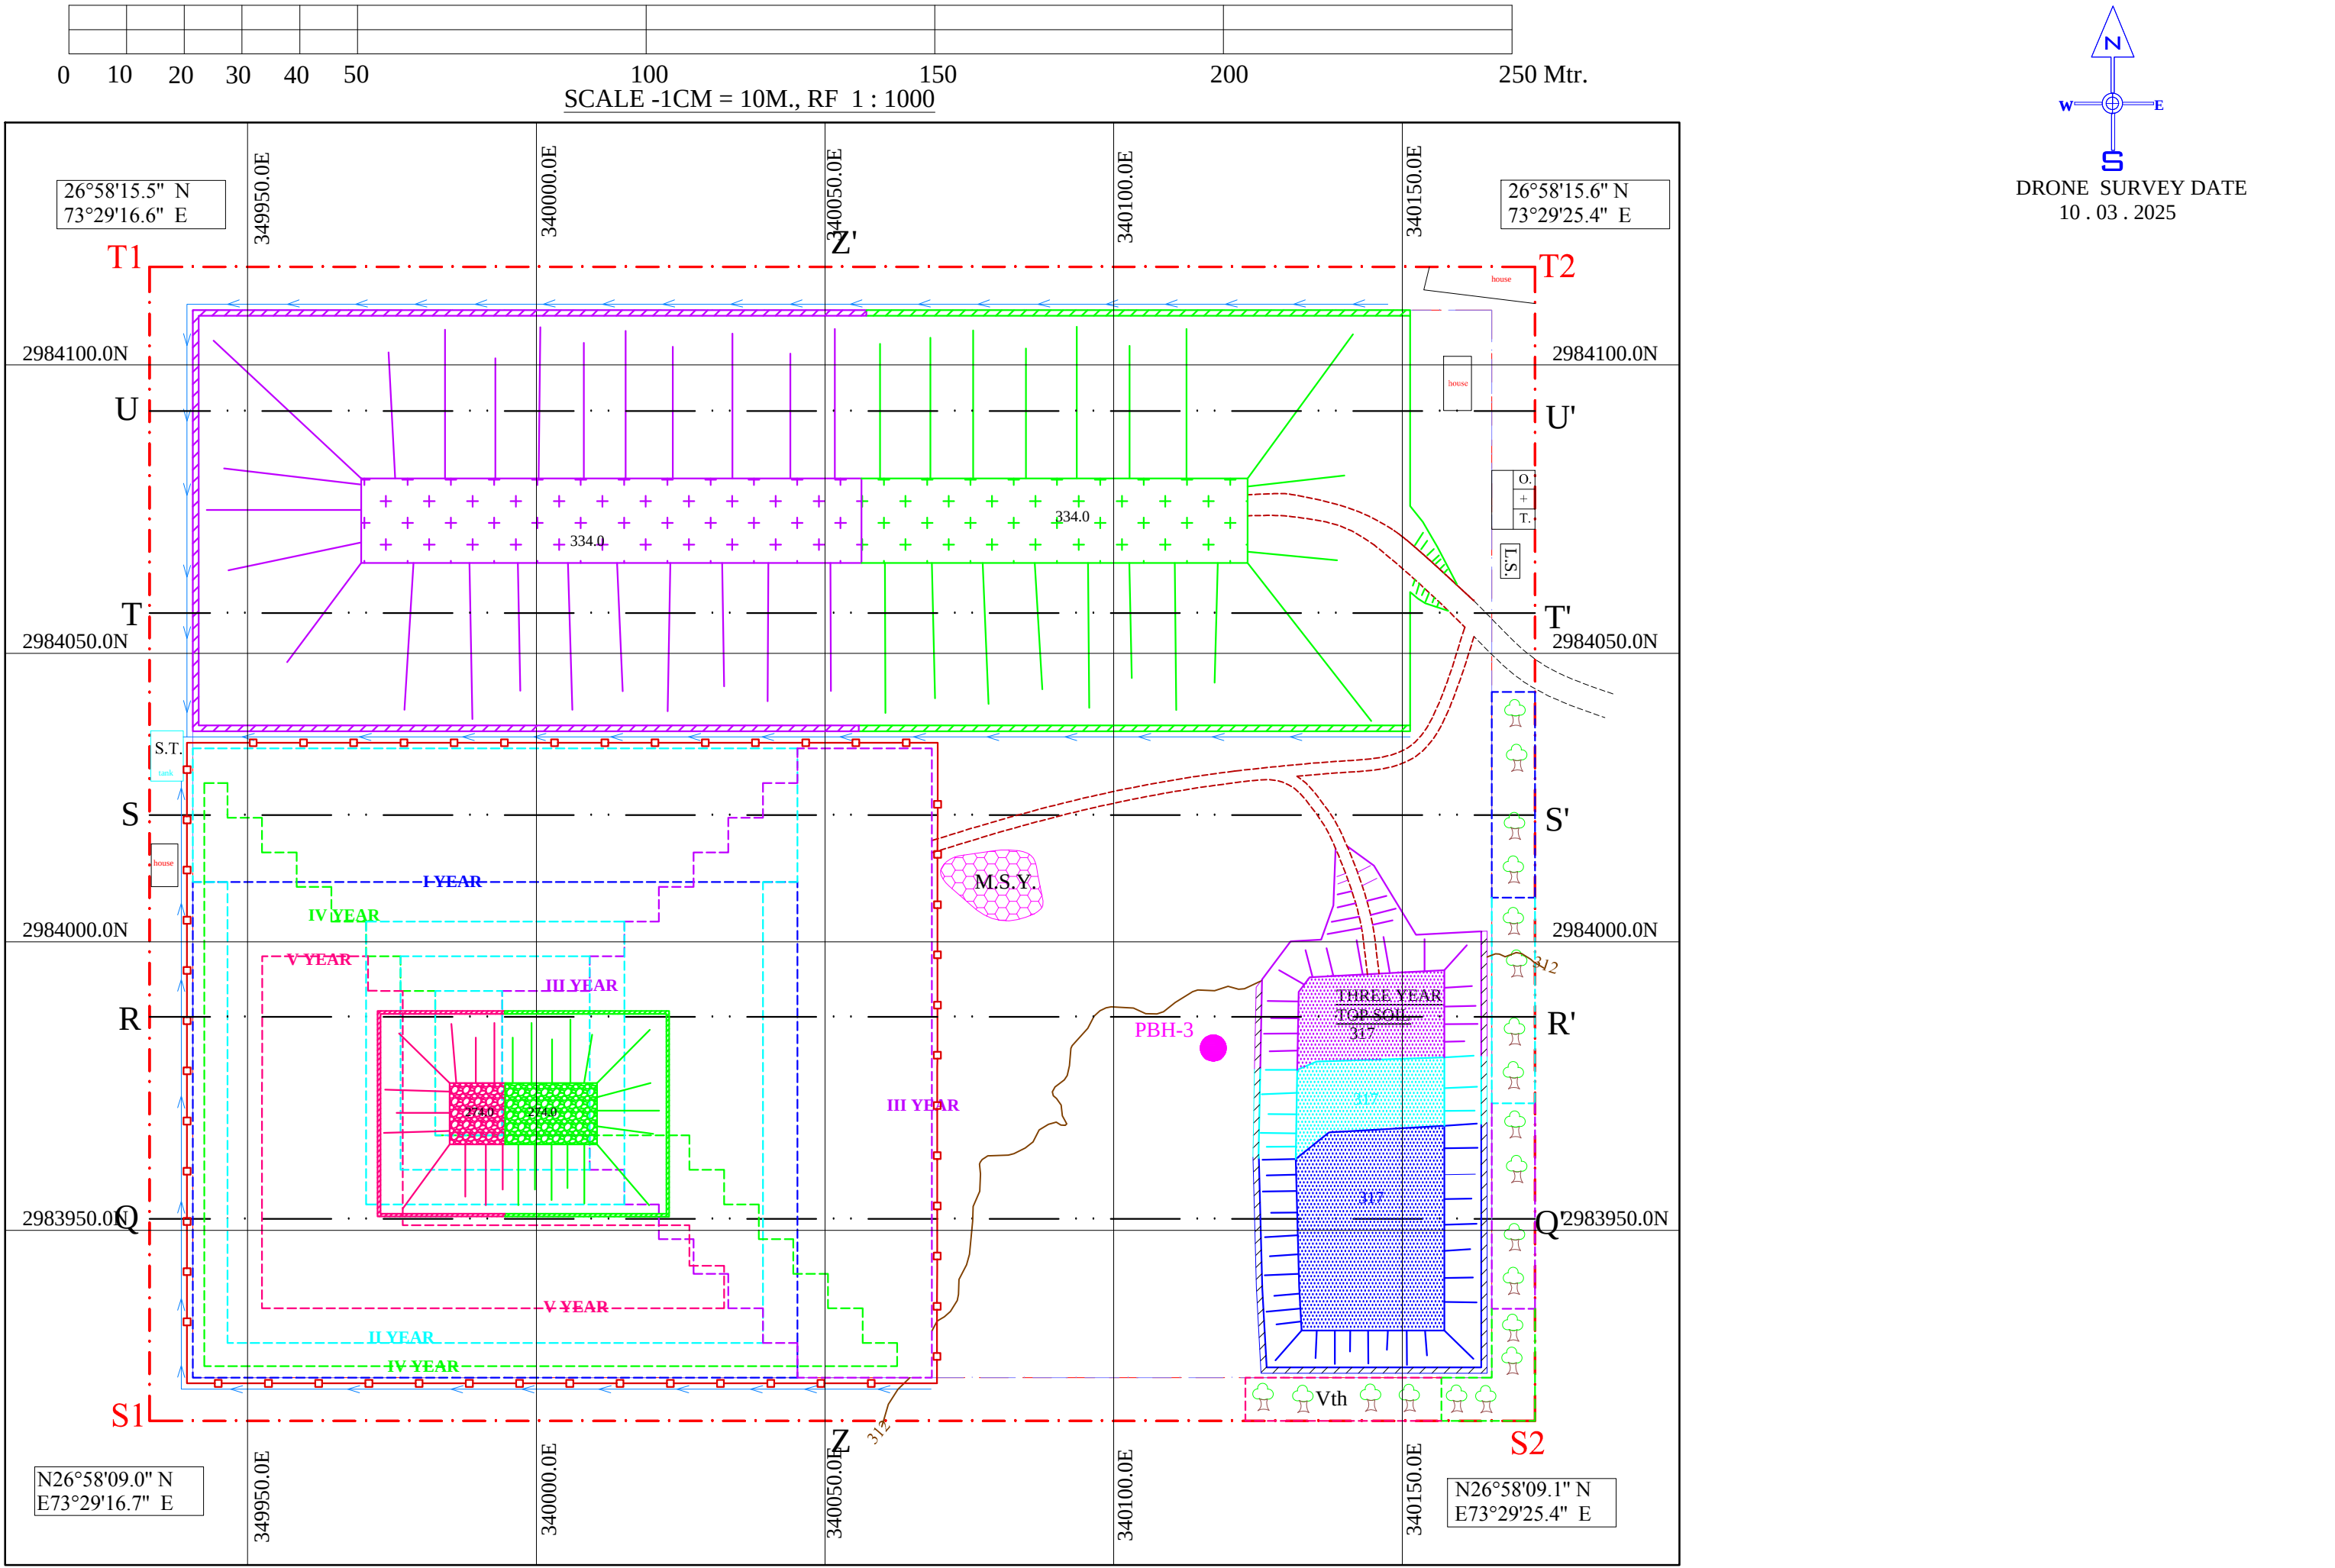


SECTION ALONG = R-R'

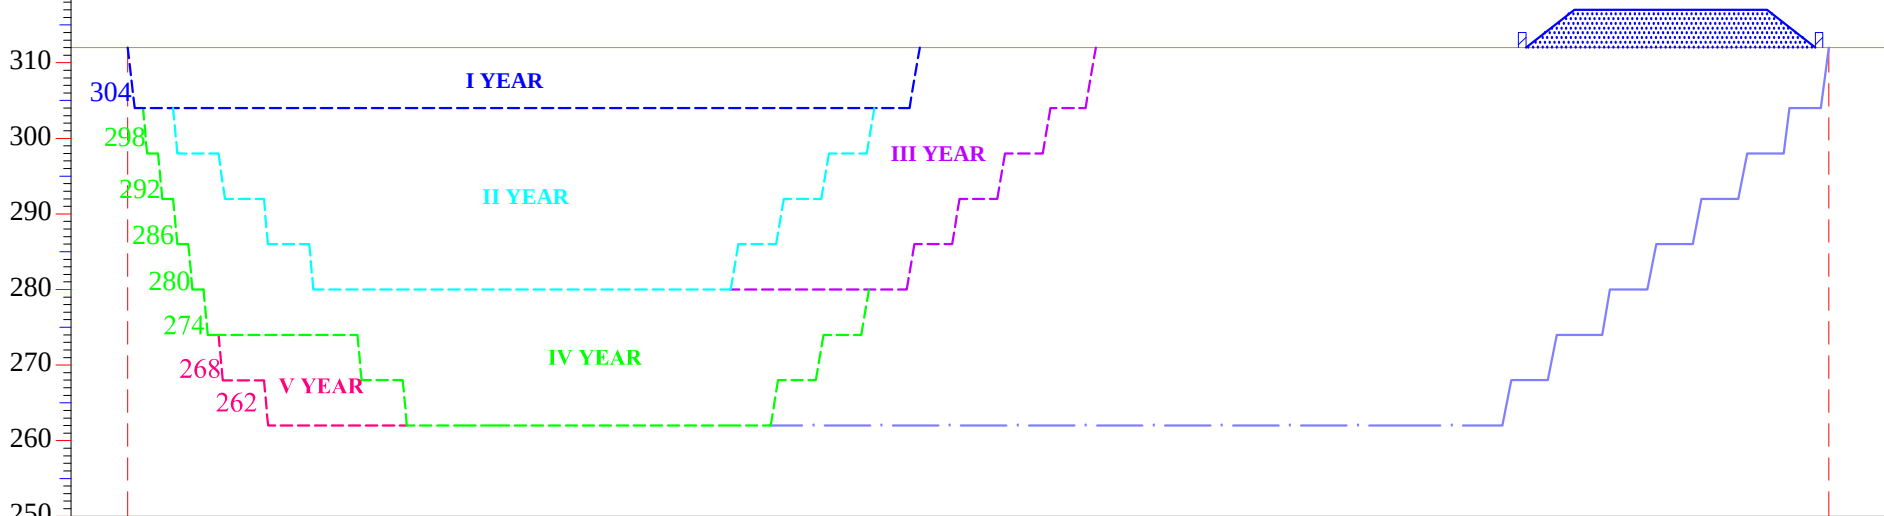


SECTION ALONG = Q-Q'

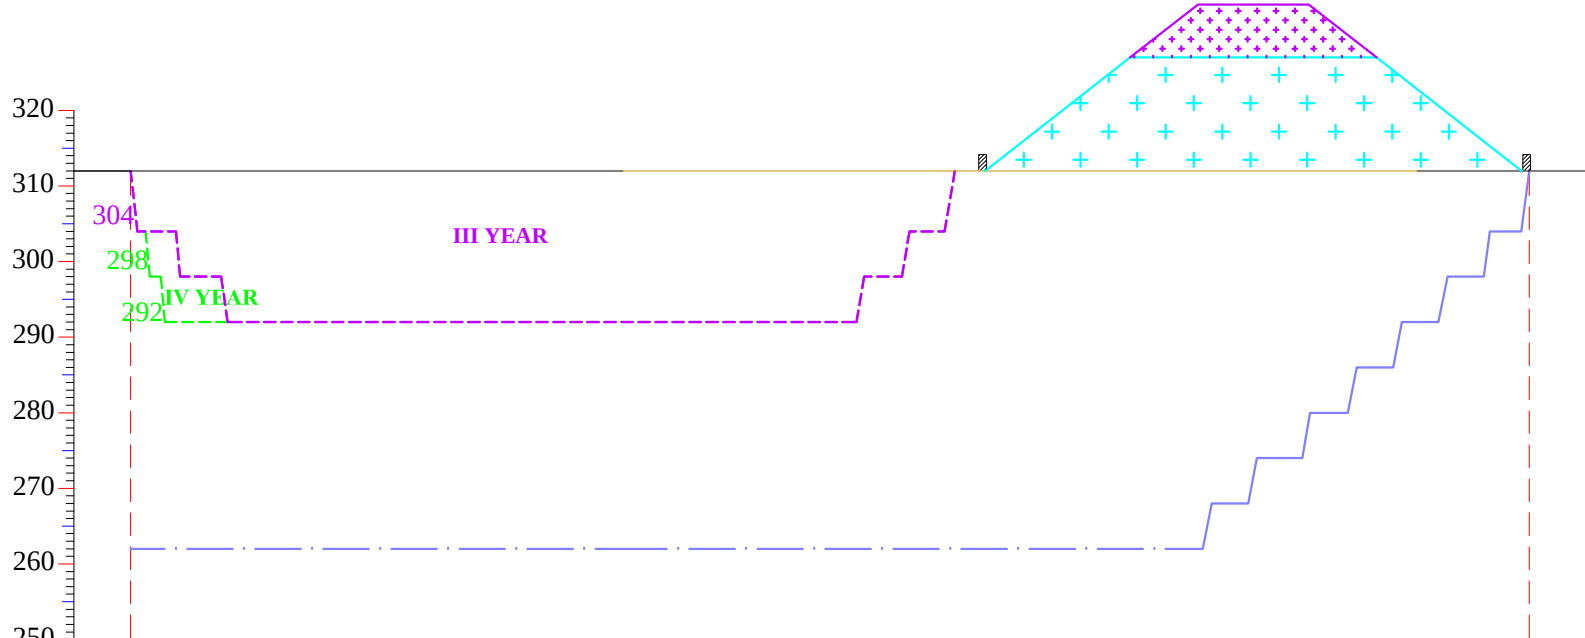


SECTION ALONG = Z-Z'

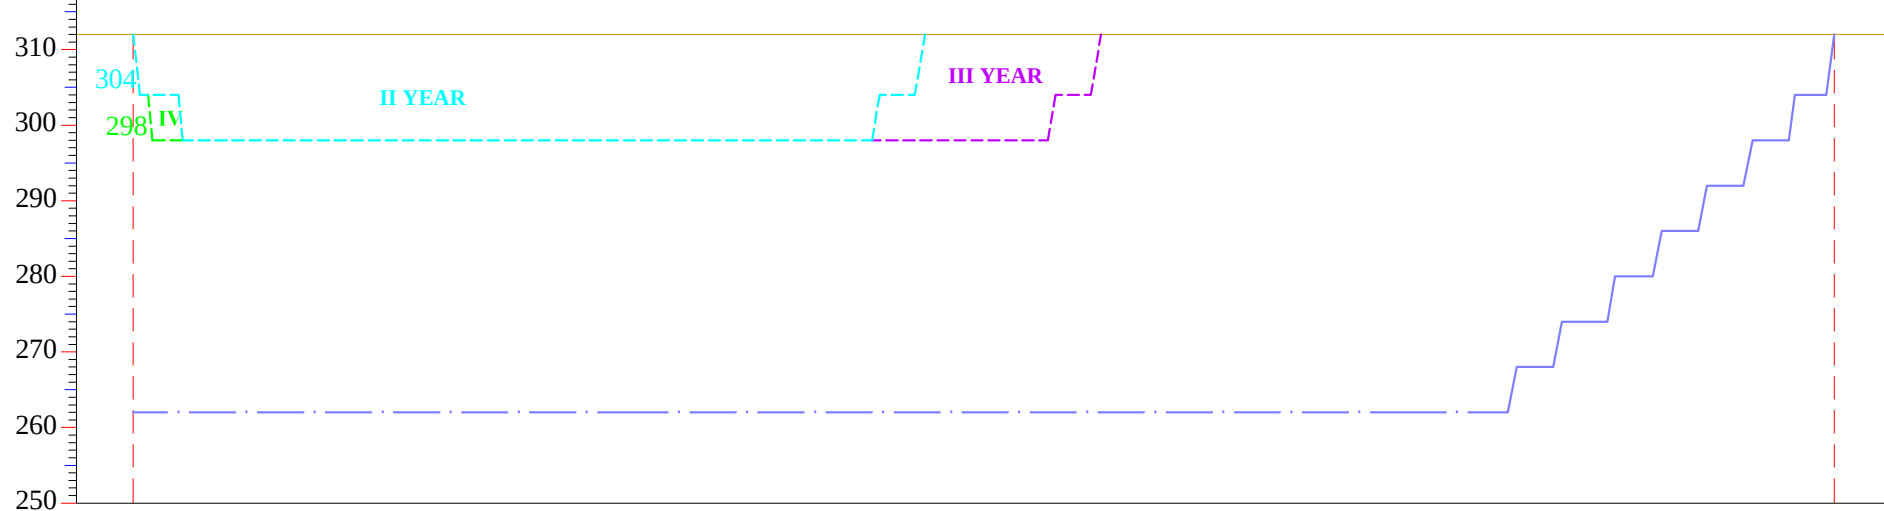

SECTION ALONG = S-S'

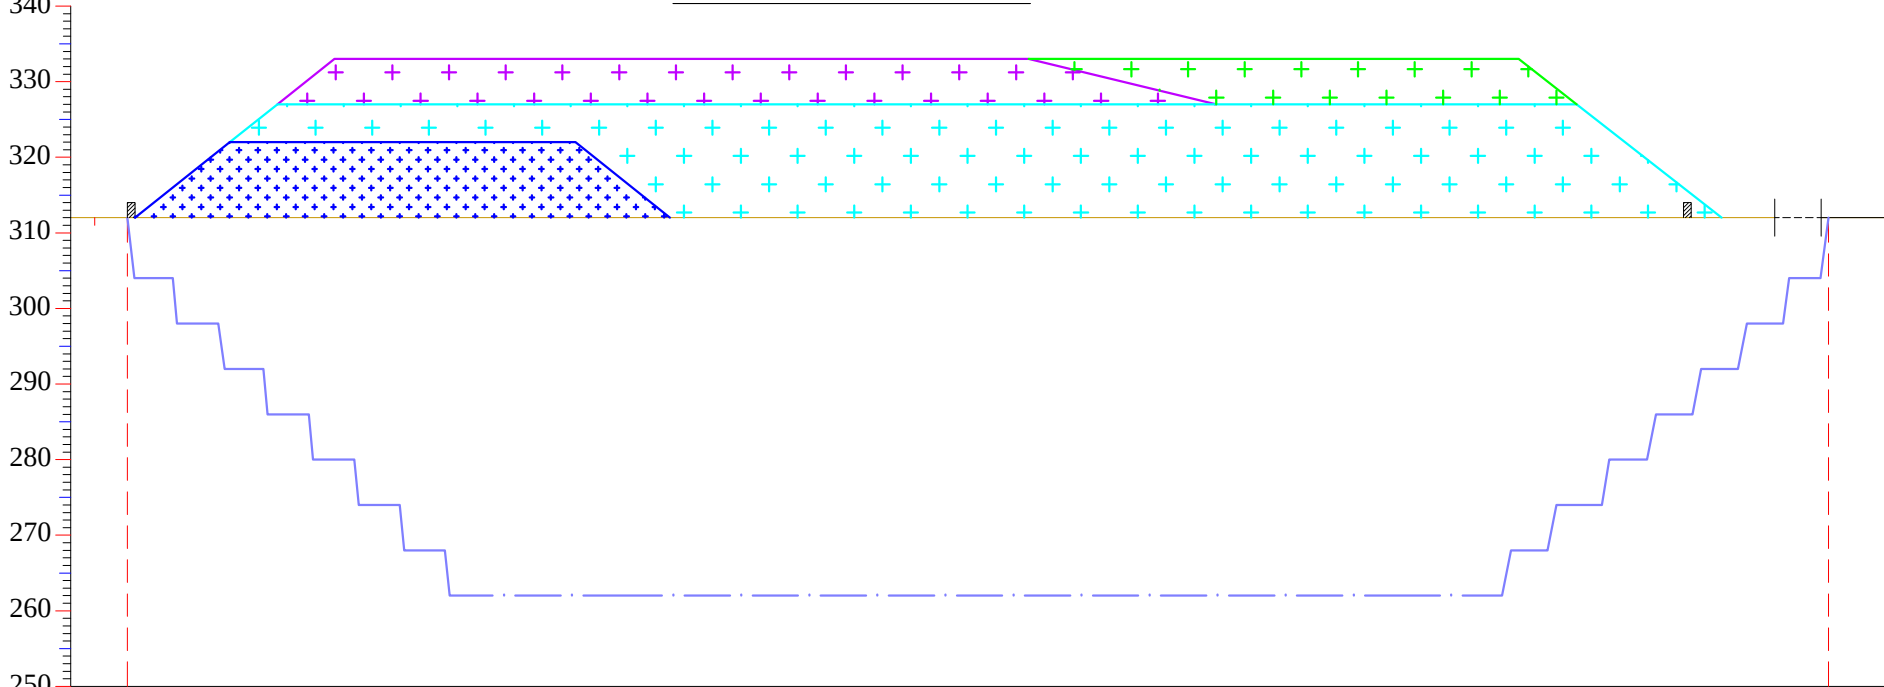

SECTION ALONG = T-T'

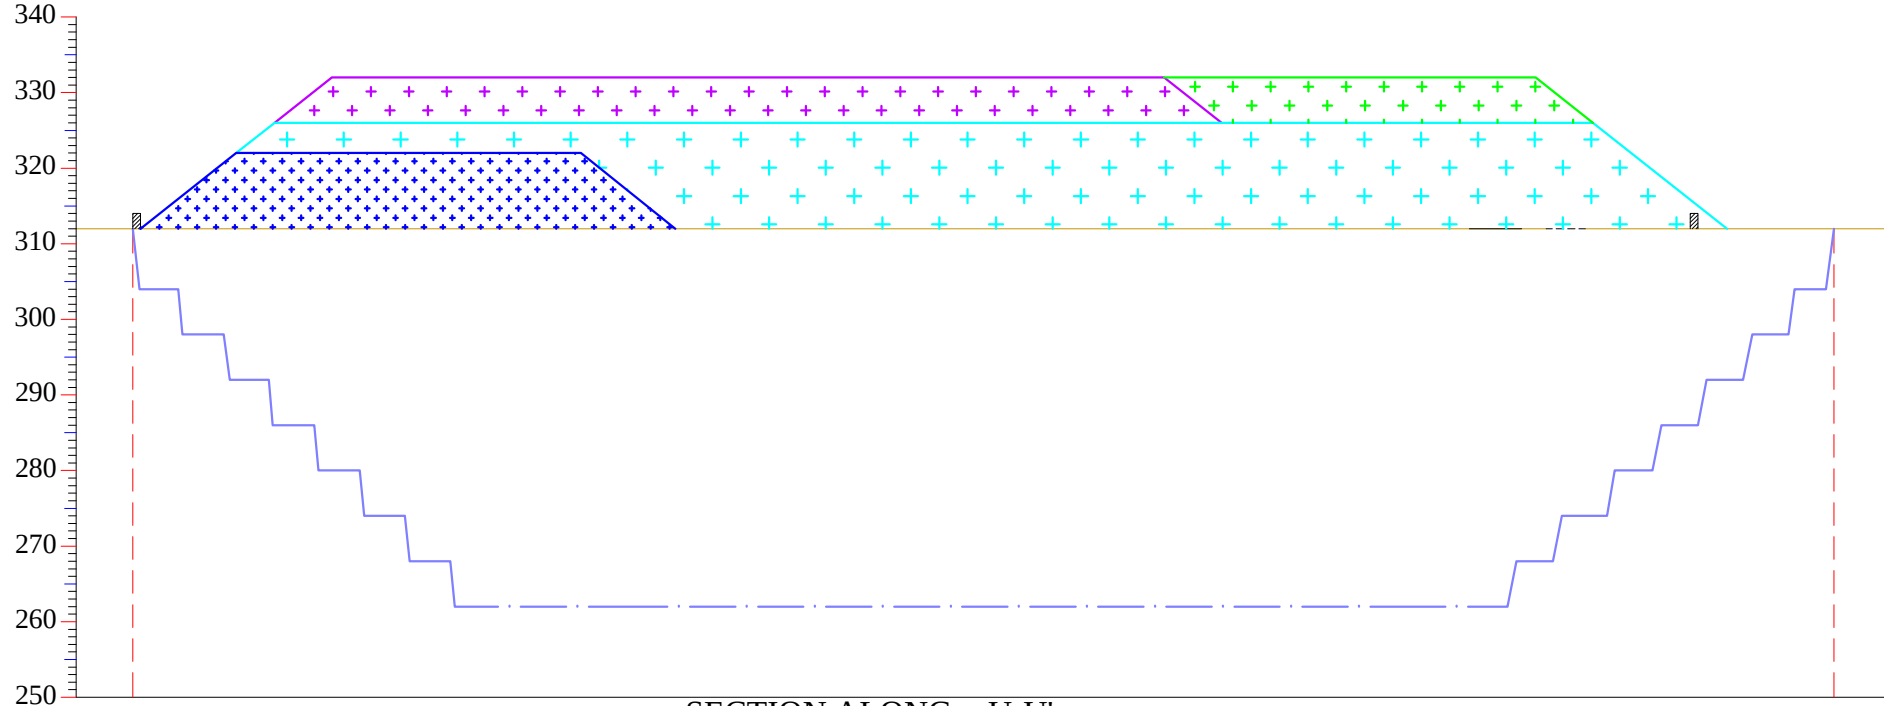

SECTION ALONG = U-U'

INDEX

	BLOCK BOUNDARY
	7.5M. STATUTORY BARRIER
	CONTOUR
	GEO-COORDINATES (S2 Pillar)
	GRID LINE (UTM WGS 84)
	ROAD / RASTA
	SECTION LINE
	EXISTING INFRASTRUCTURE
	ULTIMATE PIT LIMIT
	PROP. MINERAL STACK YARD
	PROP. HAULAGE ROAD (1:16)
	PROP. GARLAND DRAIN
	PROPOSED SETTING TANK
	PROPOSED FENCING
	PROPOSED OFFICE COMPLEX
	PROPOSED LABOUR SHED
	PROPOSED BORE HOLE

PROP. YEAR WISE TOP SOIL STACK YARD



PROP. YEAR WISE OVERBURDEN



PROP. YEAR WISE BACK FILL OVERBURDEN



PROP. YEAR WISE PIT LIMIT



PROP. YEAR WISE PLANTATION



PROPOSED FIVE YEAR RETAINING WALL



PROGRESSIVE MINE CLOSURE PLAN & SECTIONS OF HARIPURA LIMESTONE BLOCK TKS- 18 FOR AREA OF 4.800 HECT.

N/v - Haripura, Tehsil -Kheenvsar , Distt.- **Nagaur** (Raj.)
Mineral - Limestone
Applicant - M/s. Suncity Chemical & Minerals Private Limited
Area - 4.800 Hect. , Scale - 1 : 1000

PLATE NO.- 6

THIS IS CERTIFIED THAT THE PLAN IS PREPARED BASED ON THE BLOCK MAP AUTHENTICATED BY THE STATE GOVT. AND ARE CORRECT TO THE BEST OF MY KNOWLEDGE

Nimish Singhwi
Digitally signed by Nimish Singhwi
Date: 2025.05.31 17:52:39 -07'00'

QUALIFIED PERSON
MINING ENGINEER