0 10 20 30 40 50 100 150 200 250 Mtr.

SCALE -1CM = 10M., RF 1 : 1000

N

W E

S

DRONE SURVEY DATE
10 . 03 . 2025

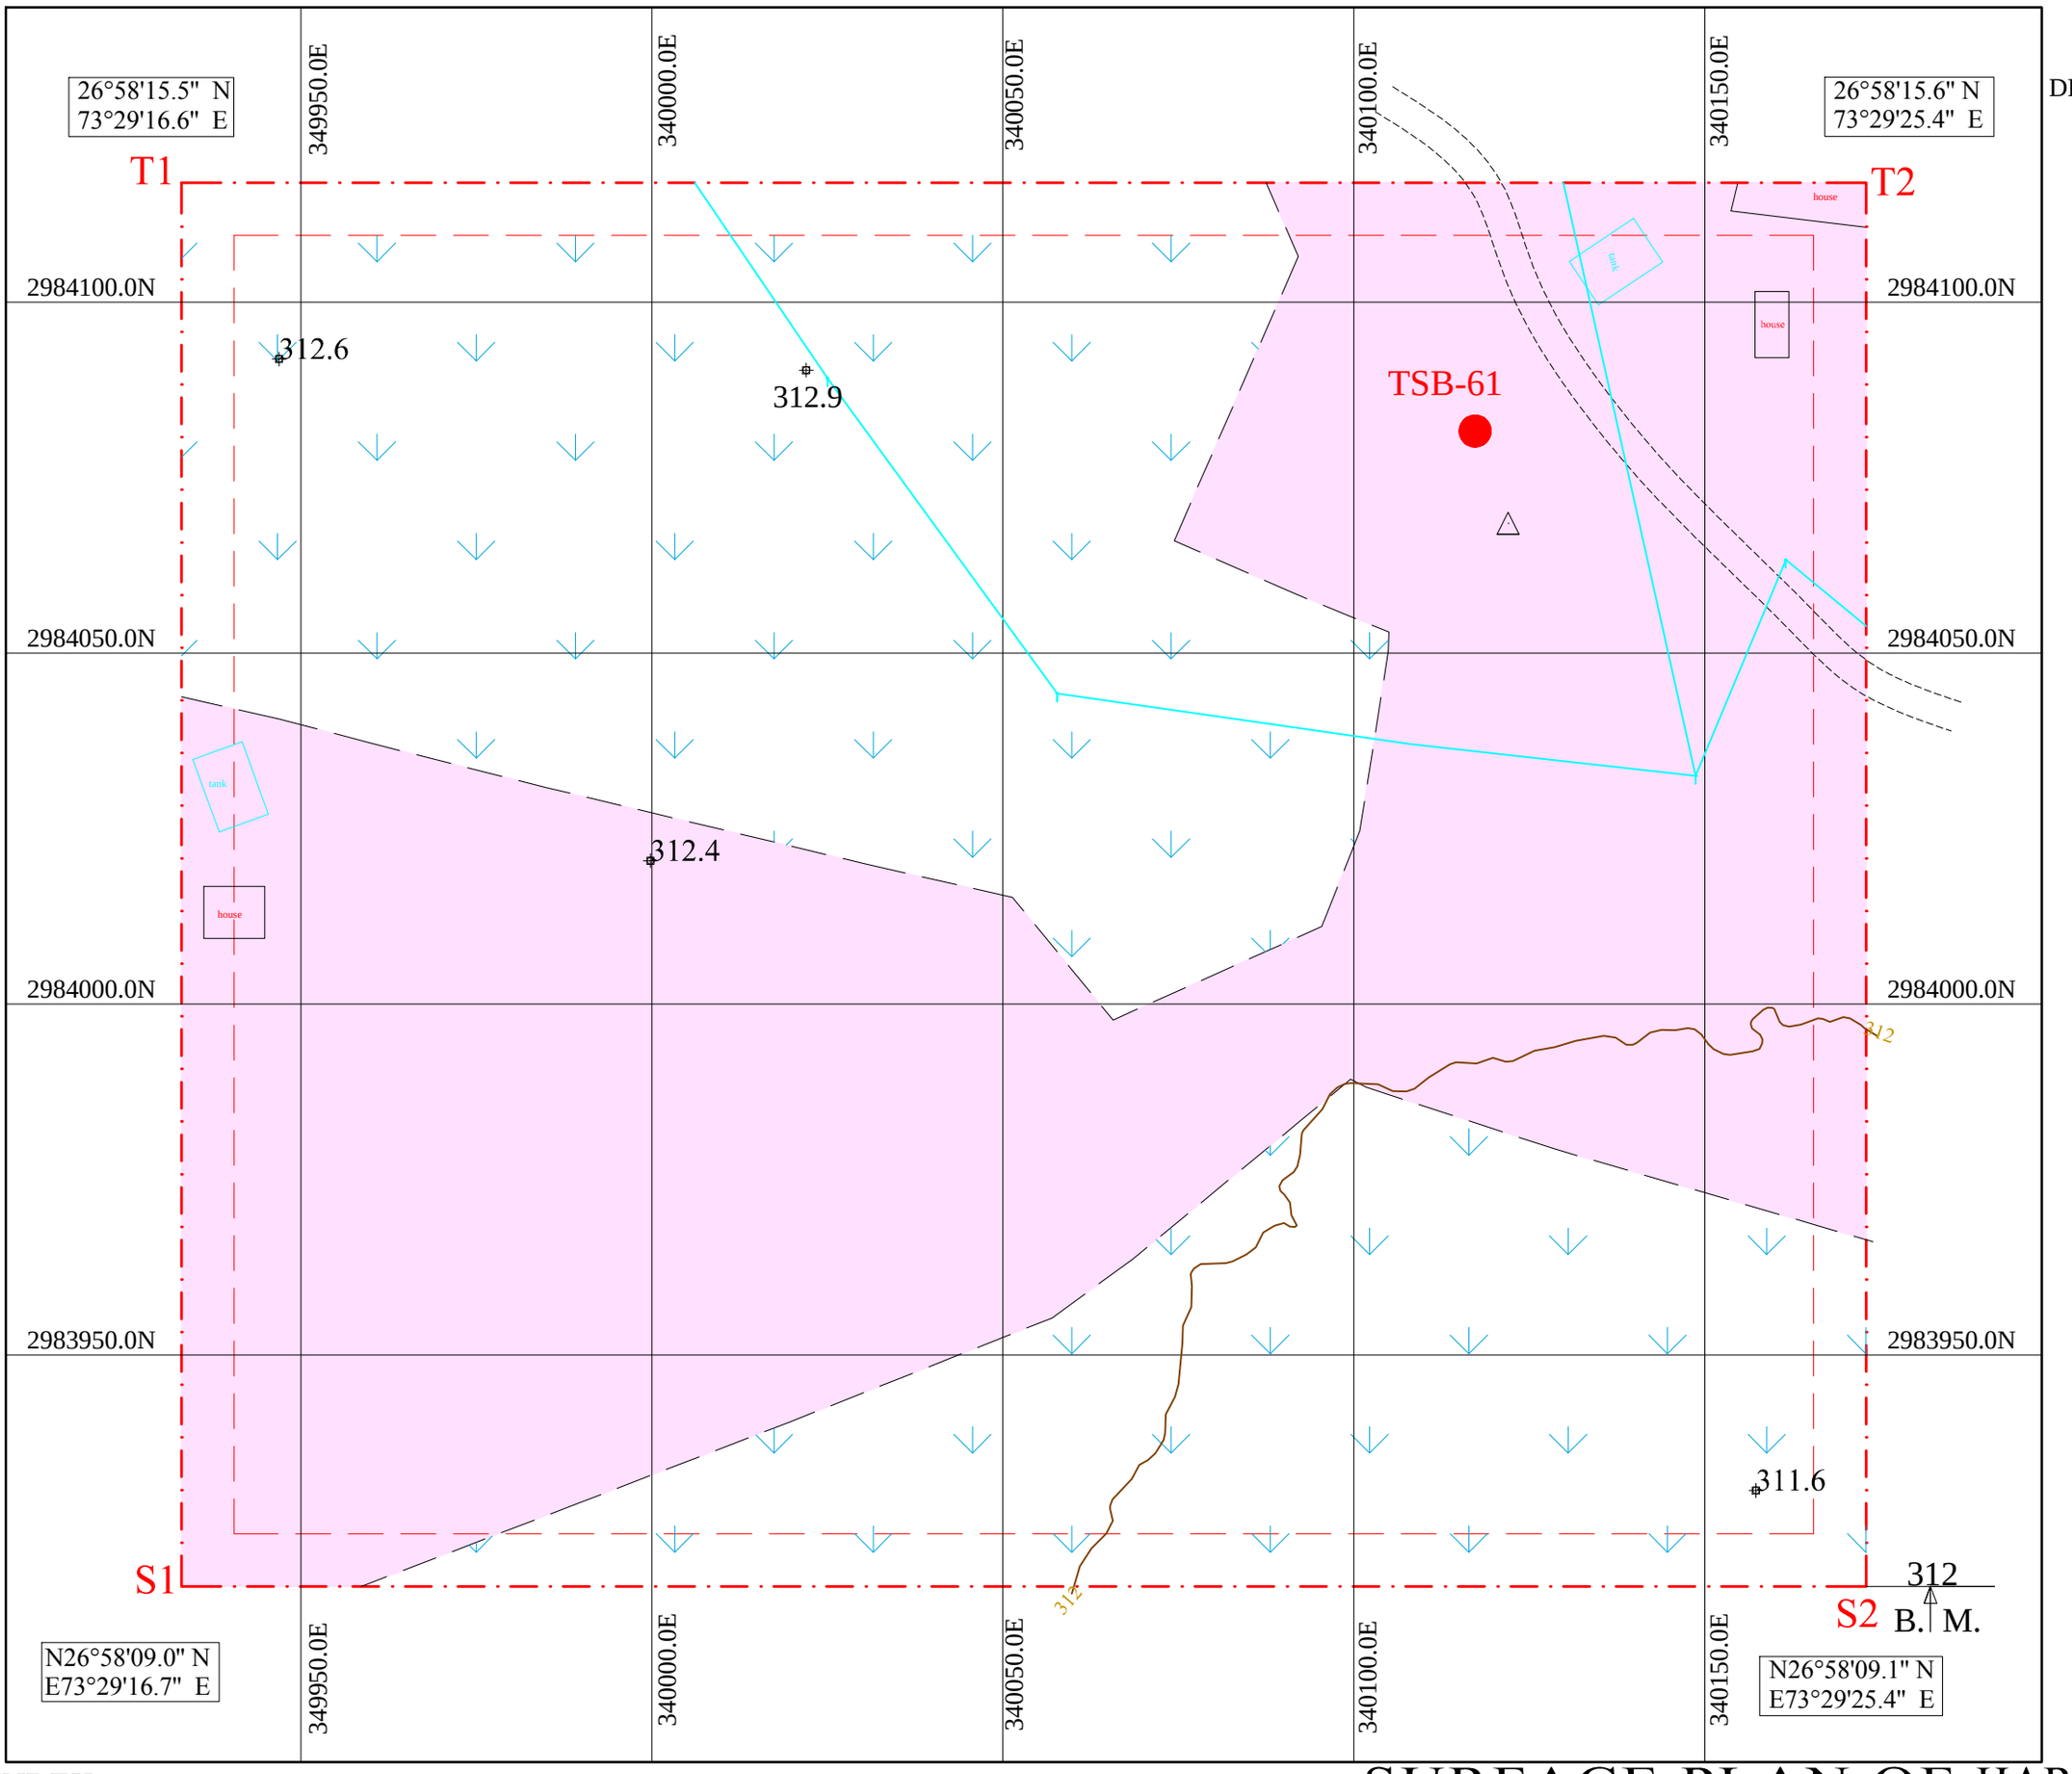

INDEX

	BLOCK BOUNDARY
	7.5 M. STATUTORY BARRIER
312	CONTOUR
312 B.M.	BENCH MARK (PILLAR - S2)
△	SURVEY STATION
ON ON	GRID LINE (UTM WGS 84)
	MINE ROAD
N26°58'09.1" N E73°29'25.4" E	GEO-COORDINATES (S2 Pillar)
	GOVT. LAND (2.6456 Hect.)
	PVT. LAND (2.1544 Hect.)
TSB-61	EXISTING BORE HOLE
	EXISTING TANK
	EXISTING INFRASTRUCTURE
	EXISTING ELECTRIC LINE
311.6	SPOT MRL

SURFACE PLAN OF HARIPURA LIMESTONE BLOCK TKSB-18 FOR AREA OF 4.800 HECT.

N\v - Haripura, Tehsil -Kheenvsar , Distt.- **Nagaur** (Raj.)
Mineral - Limestone
Applicant - M/s. Suncity Chemical & Minerals Private Limited
Area - 4.800 Hect. , Scale - 1 : 1000 PLATE NO.- 3

THIS IS CERTIFIED THAT THE PLAN IS PREPARED BASED ON THE BLOCK MAP AUTHENTICATED BY THE STATE GOVT. AND ARE CORRECT TO THE BEST OF MY KNOWLEDGE

Nimish Singhwi
Digitally signed by Nimish Singhwi
Date: 2025.05.31 17:48:05 -07'00'

QUALIFIED PERSON
MINING ENGINEER